

# 改造与更新

## 分点改造

岩前剧场

· · · · ·


建设以酒堂文化为中心衍生的多功能的公共空间

# 场地选址



## 原联星一酒堂、旧厨房

周边环境：周边是民居和民宿，旁边是旧厨房，对面有一块小空地，靠近大路，小路比较安静。

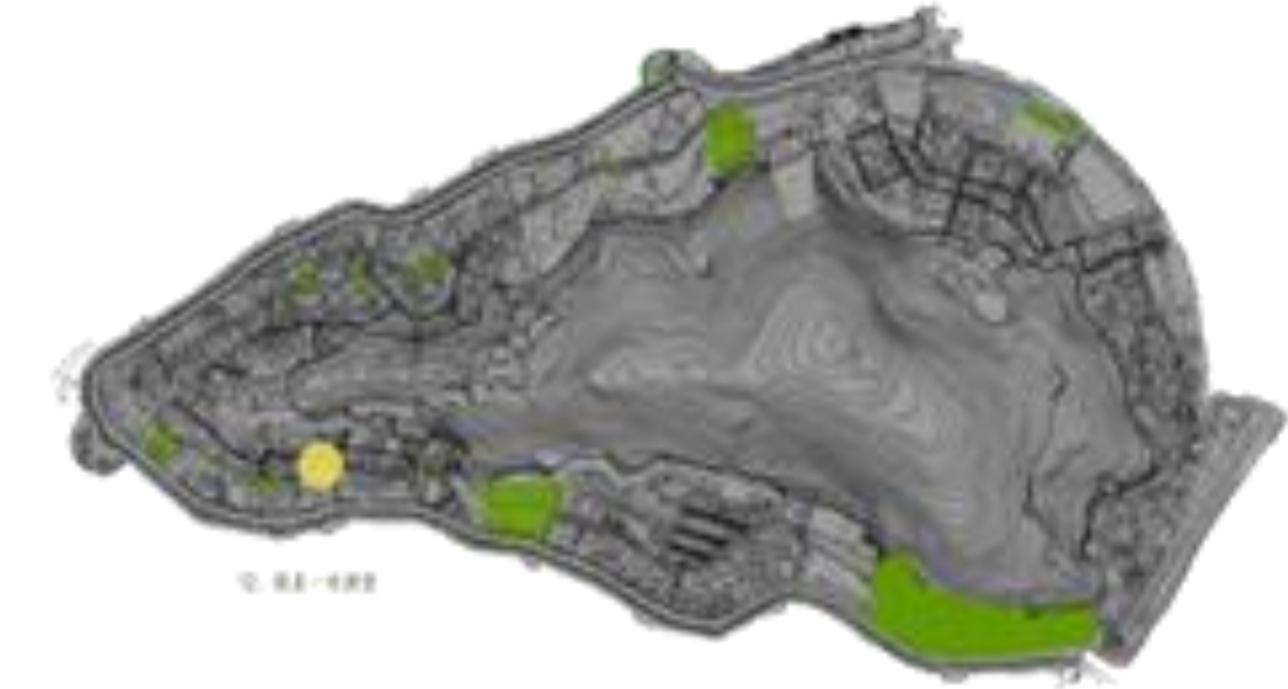

## 场地问题：

1. 机动车占道停车。
2. 楼外高压电缆。
3. 缺乏公共休闲场所。

# 岩前村酒堂



岩前村的酒堂大多已经闲置，使用率低，设施老旧，几乎废弃。

# 岩前村酒堂


改造设想：

在原建筑的基础上修复改造，增加文商旅综合体验的一系列业态，使岩前村焕发新的活力，改善岩前村的旅游条件及商业环境，发扬酒堂文化。

结合社区绿道，以点线面的形式打造绿色景区。

建设公共空间节点，增加绿化

提取酒堂文化元素及特色，将原有酒堂进行串联。

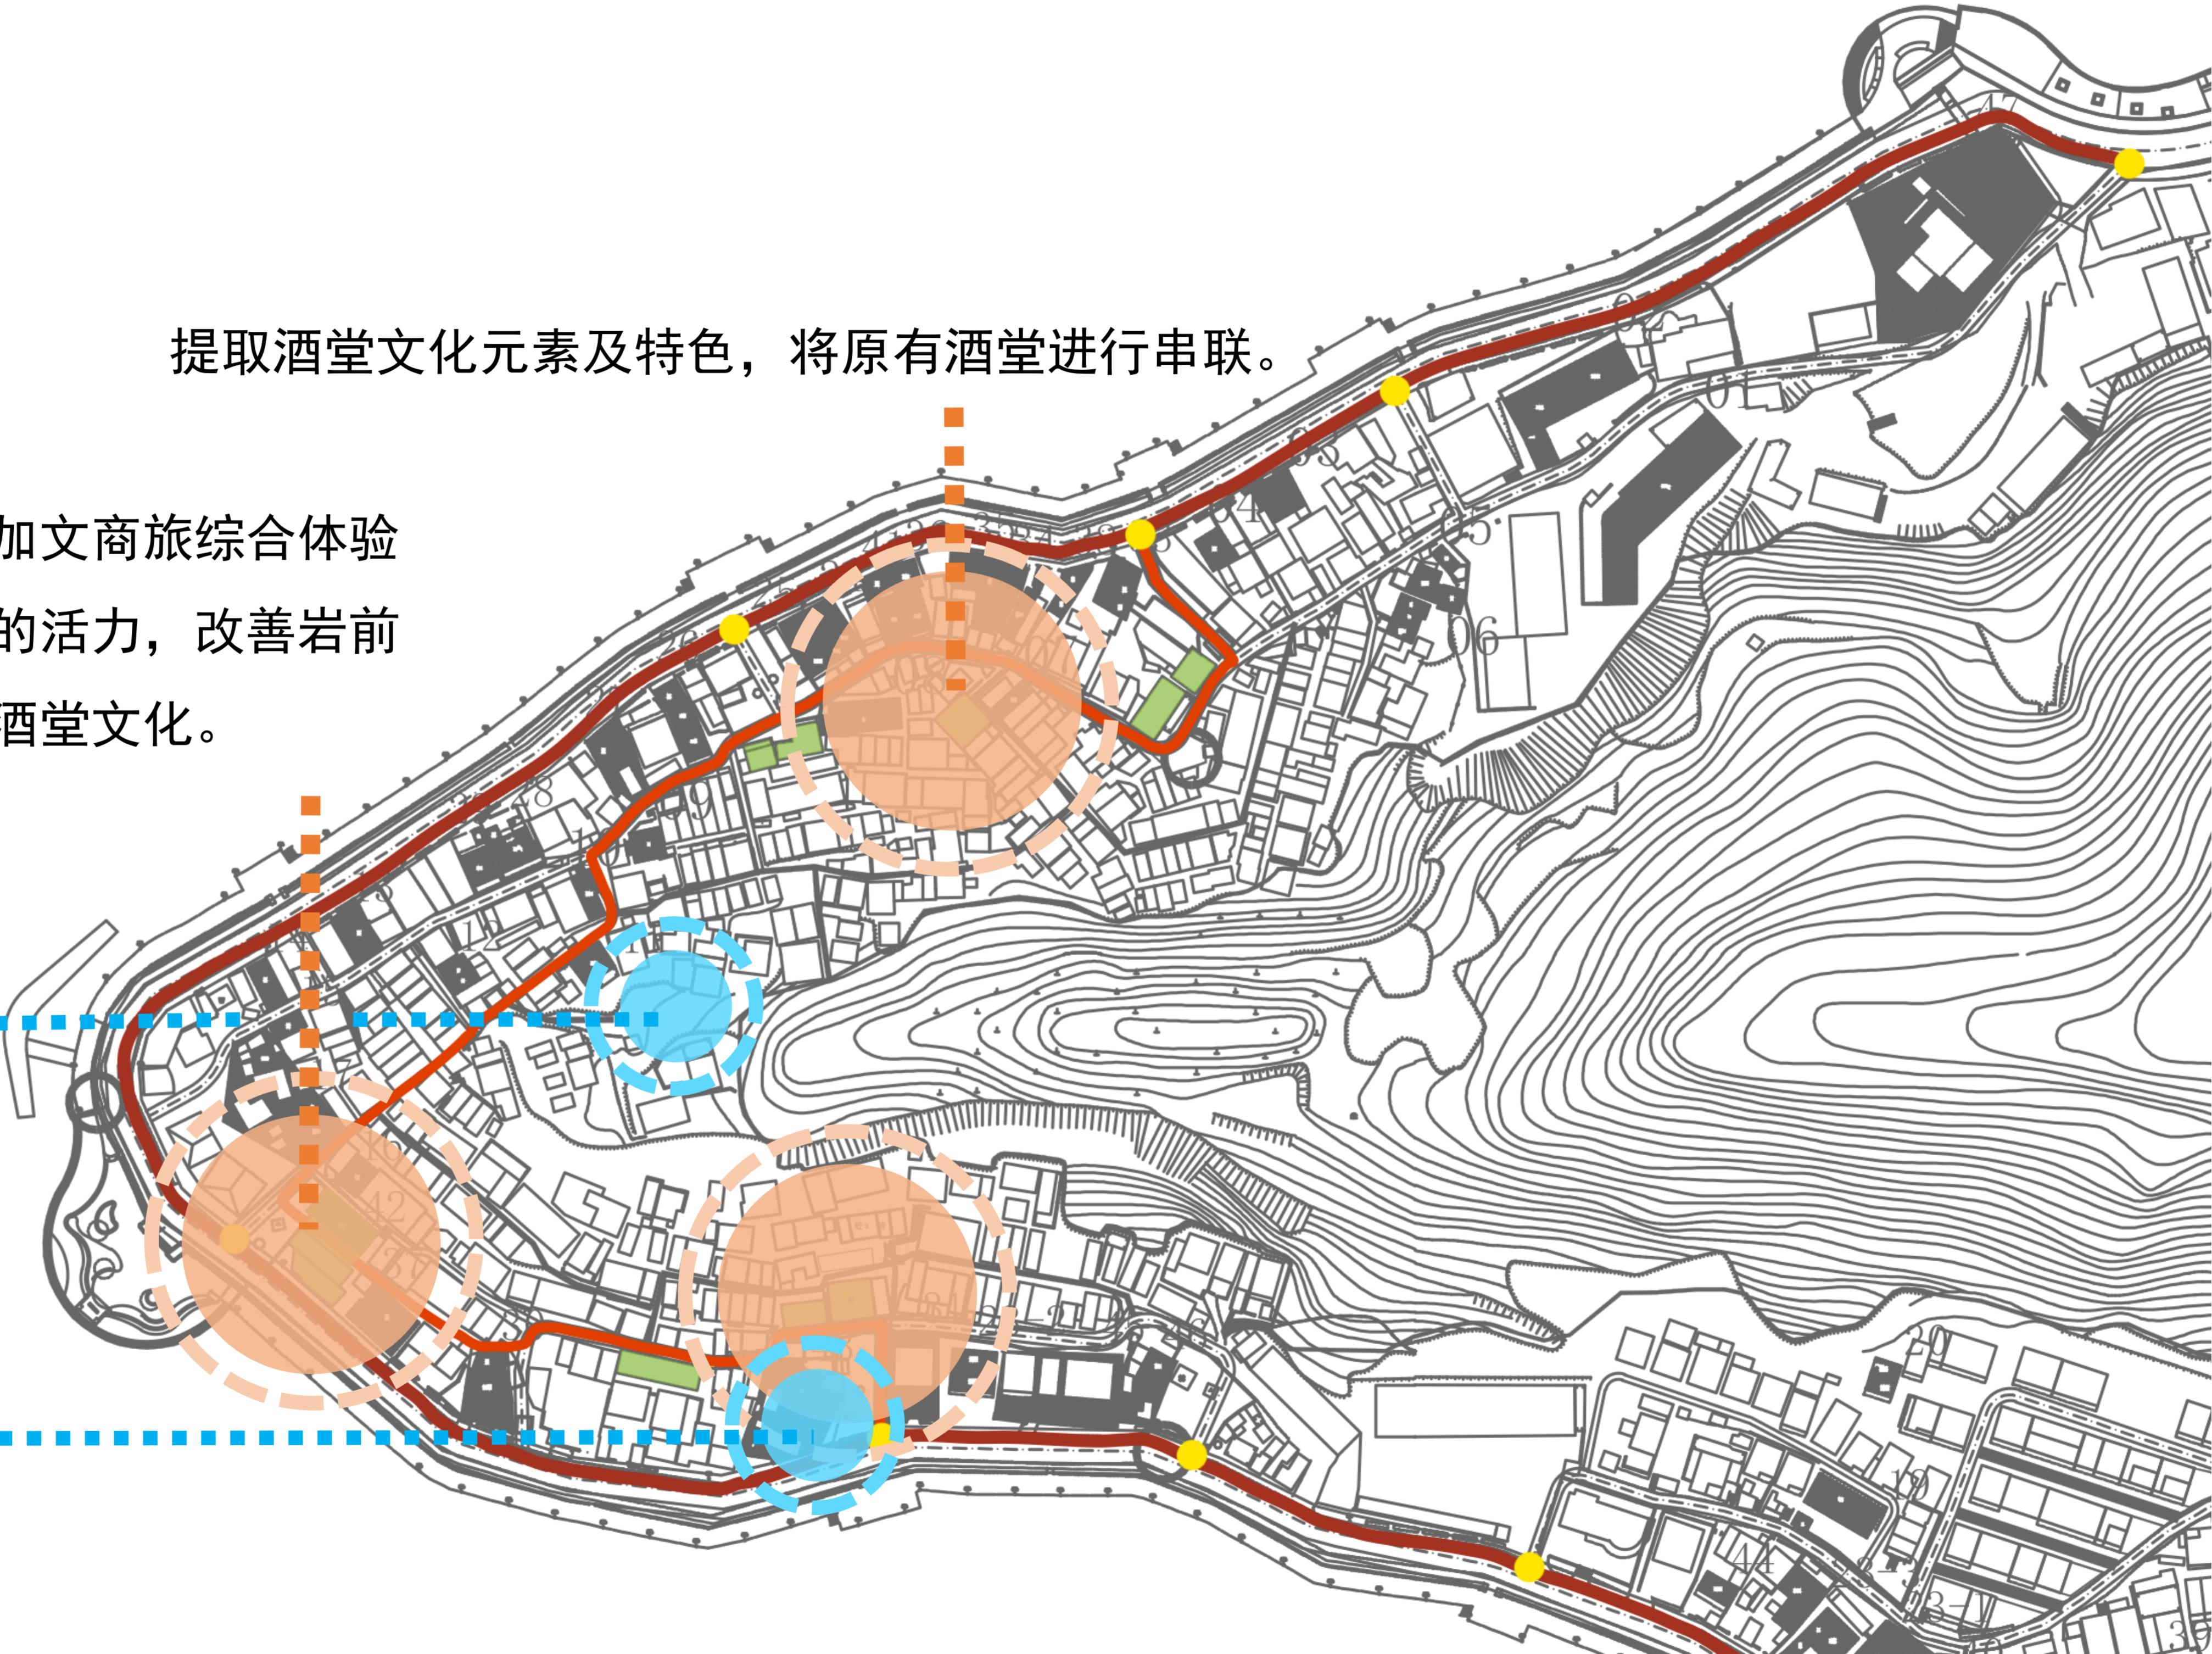

# 改造策略

· · · · ·

以酒堂文化为中心衍生的多功能剧场公共空间



# 改造策略

## 小型剧场

提炼酒堂作为文化活动中心、开展文体演出活动的功能，建设以酒堂文化为中心衍生的多功能剧场公共空间。

.....




# 改造策略

## 小型剧场

### 1. 举行文旅演出，体验地方特色文化。

粤剧《龙母传奇》根据德庆悦城龙母的故事创作，具有本地文化特色，可以作为端口向游客进行文化输出，加深游客对肇庆的文化记忆。

.....

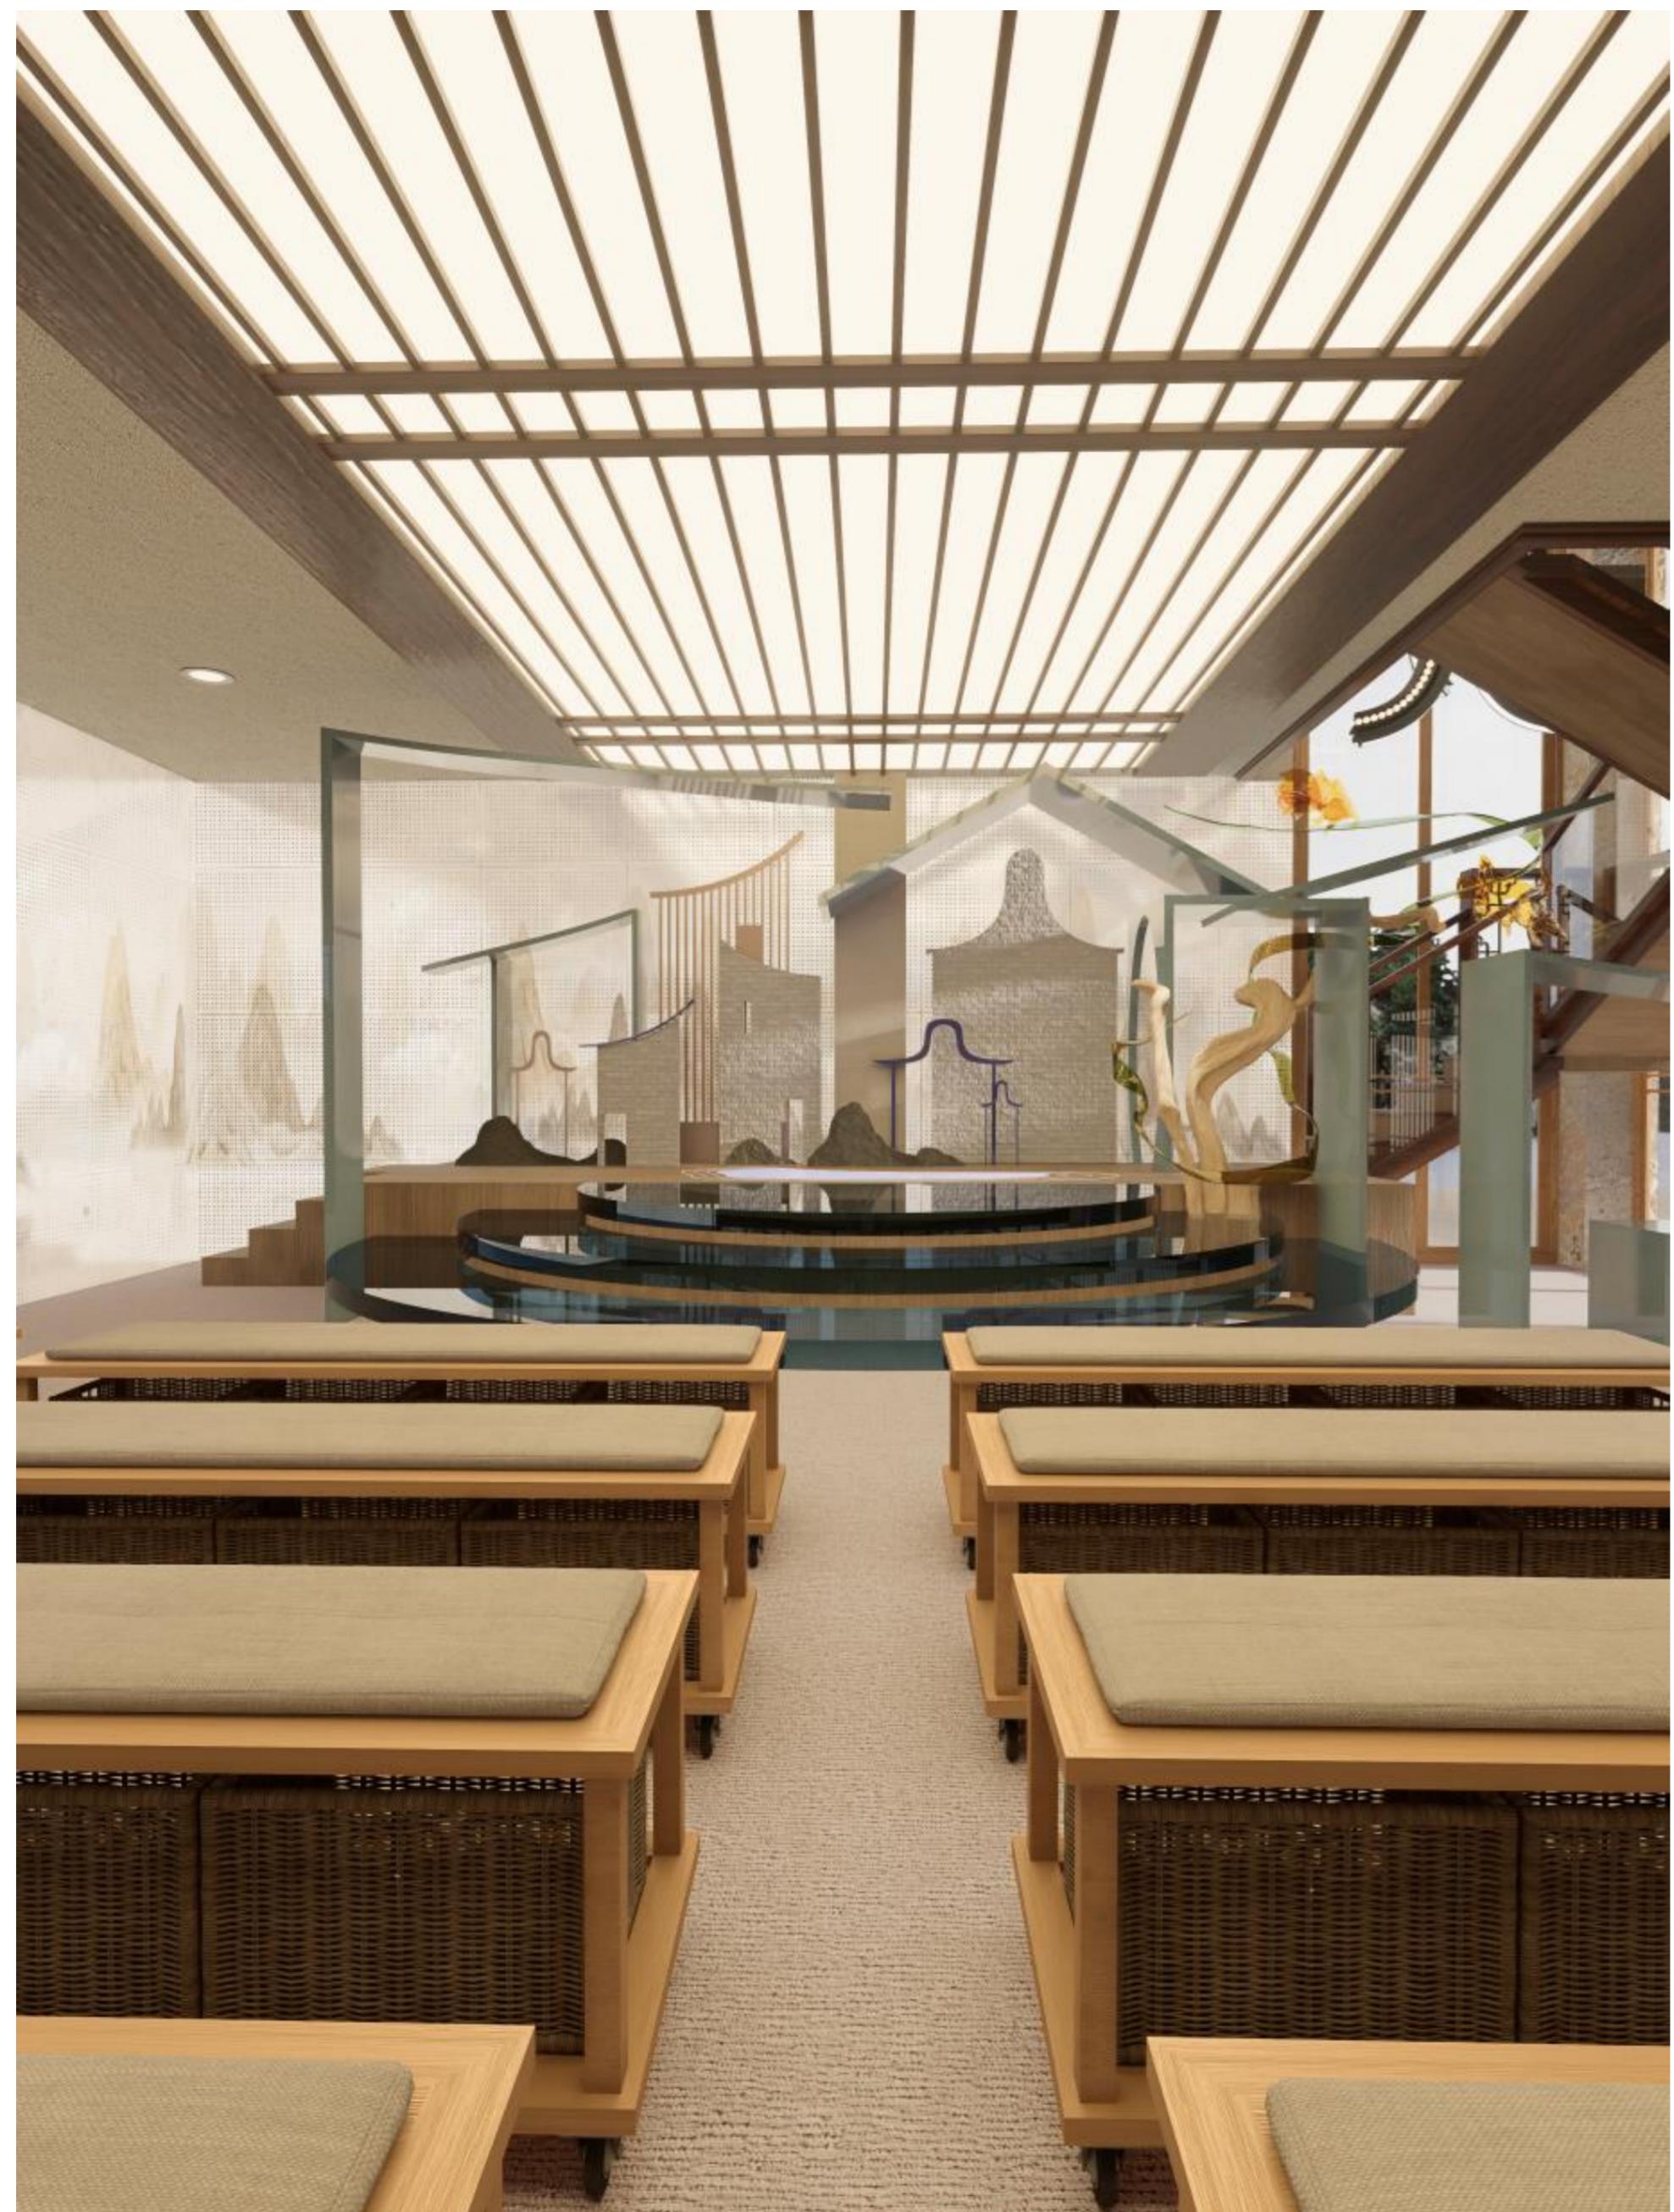

# 改造策略

## 小型剧场

2. 建设多功能的剧院空间。

开展戏剧戏曲、脱口秀、儿童剧等形式多样的演出服务。

以个性化的文化体验，有影响力的文化IP，从多个维度撬动城市文化的新动能。

.....



# 改造策略

## 小型剧场

### 3. 建设游客与本地居民都能使用的公共空间

提取酒堂可作为文化活动中心和开展文体演出活动的特点，建设多功能的公共空间。为游客提供观剧体验也为村民提供开展大型活动的空间，增加该地人群的娱乐活动。

.....

# 两种形态

闭合



在进行粤剧，脱口秀等演出时，剧场是围合的状态，满足演出的私密性。

开放



村内组织文艺汇演等活动时，剧场是打开的状态，作为一个开放的公共空间提供给村民及游客使用。



# 改造策略

## 小型剧场

### 4. 文商旅结合打造茶饮休闲空间



剧院与茶室结合提升剧院的文化品位和氛围，使其不仅仅是一个演出场所，更成为一个综合性的文化休闲胜地，从而增强其吸引力和竞争力。使游客在观看演出前后有一个放松和交流的场所，延长游客的停留时间。通过茶饮销售和休闲服务，提升剧院的经济效益。

.....

# 艺术装置

.....

模拟传统建筑风格，提供打卡功能，完善酒堂文化浏览线内容。

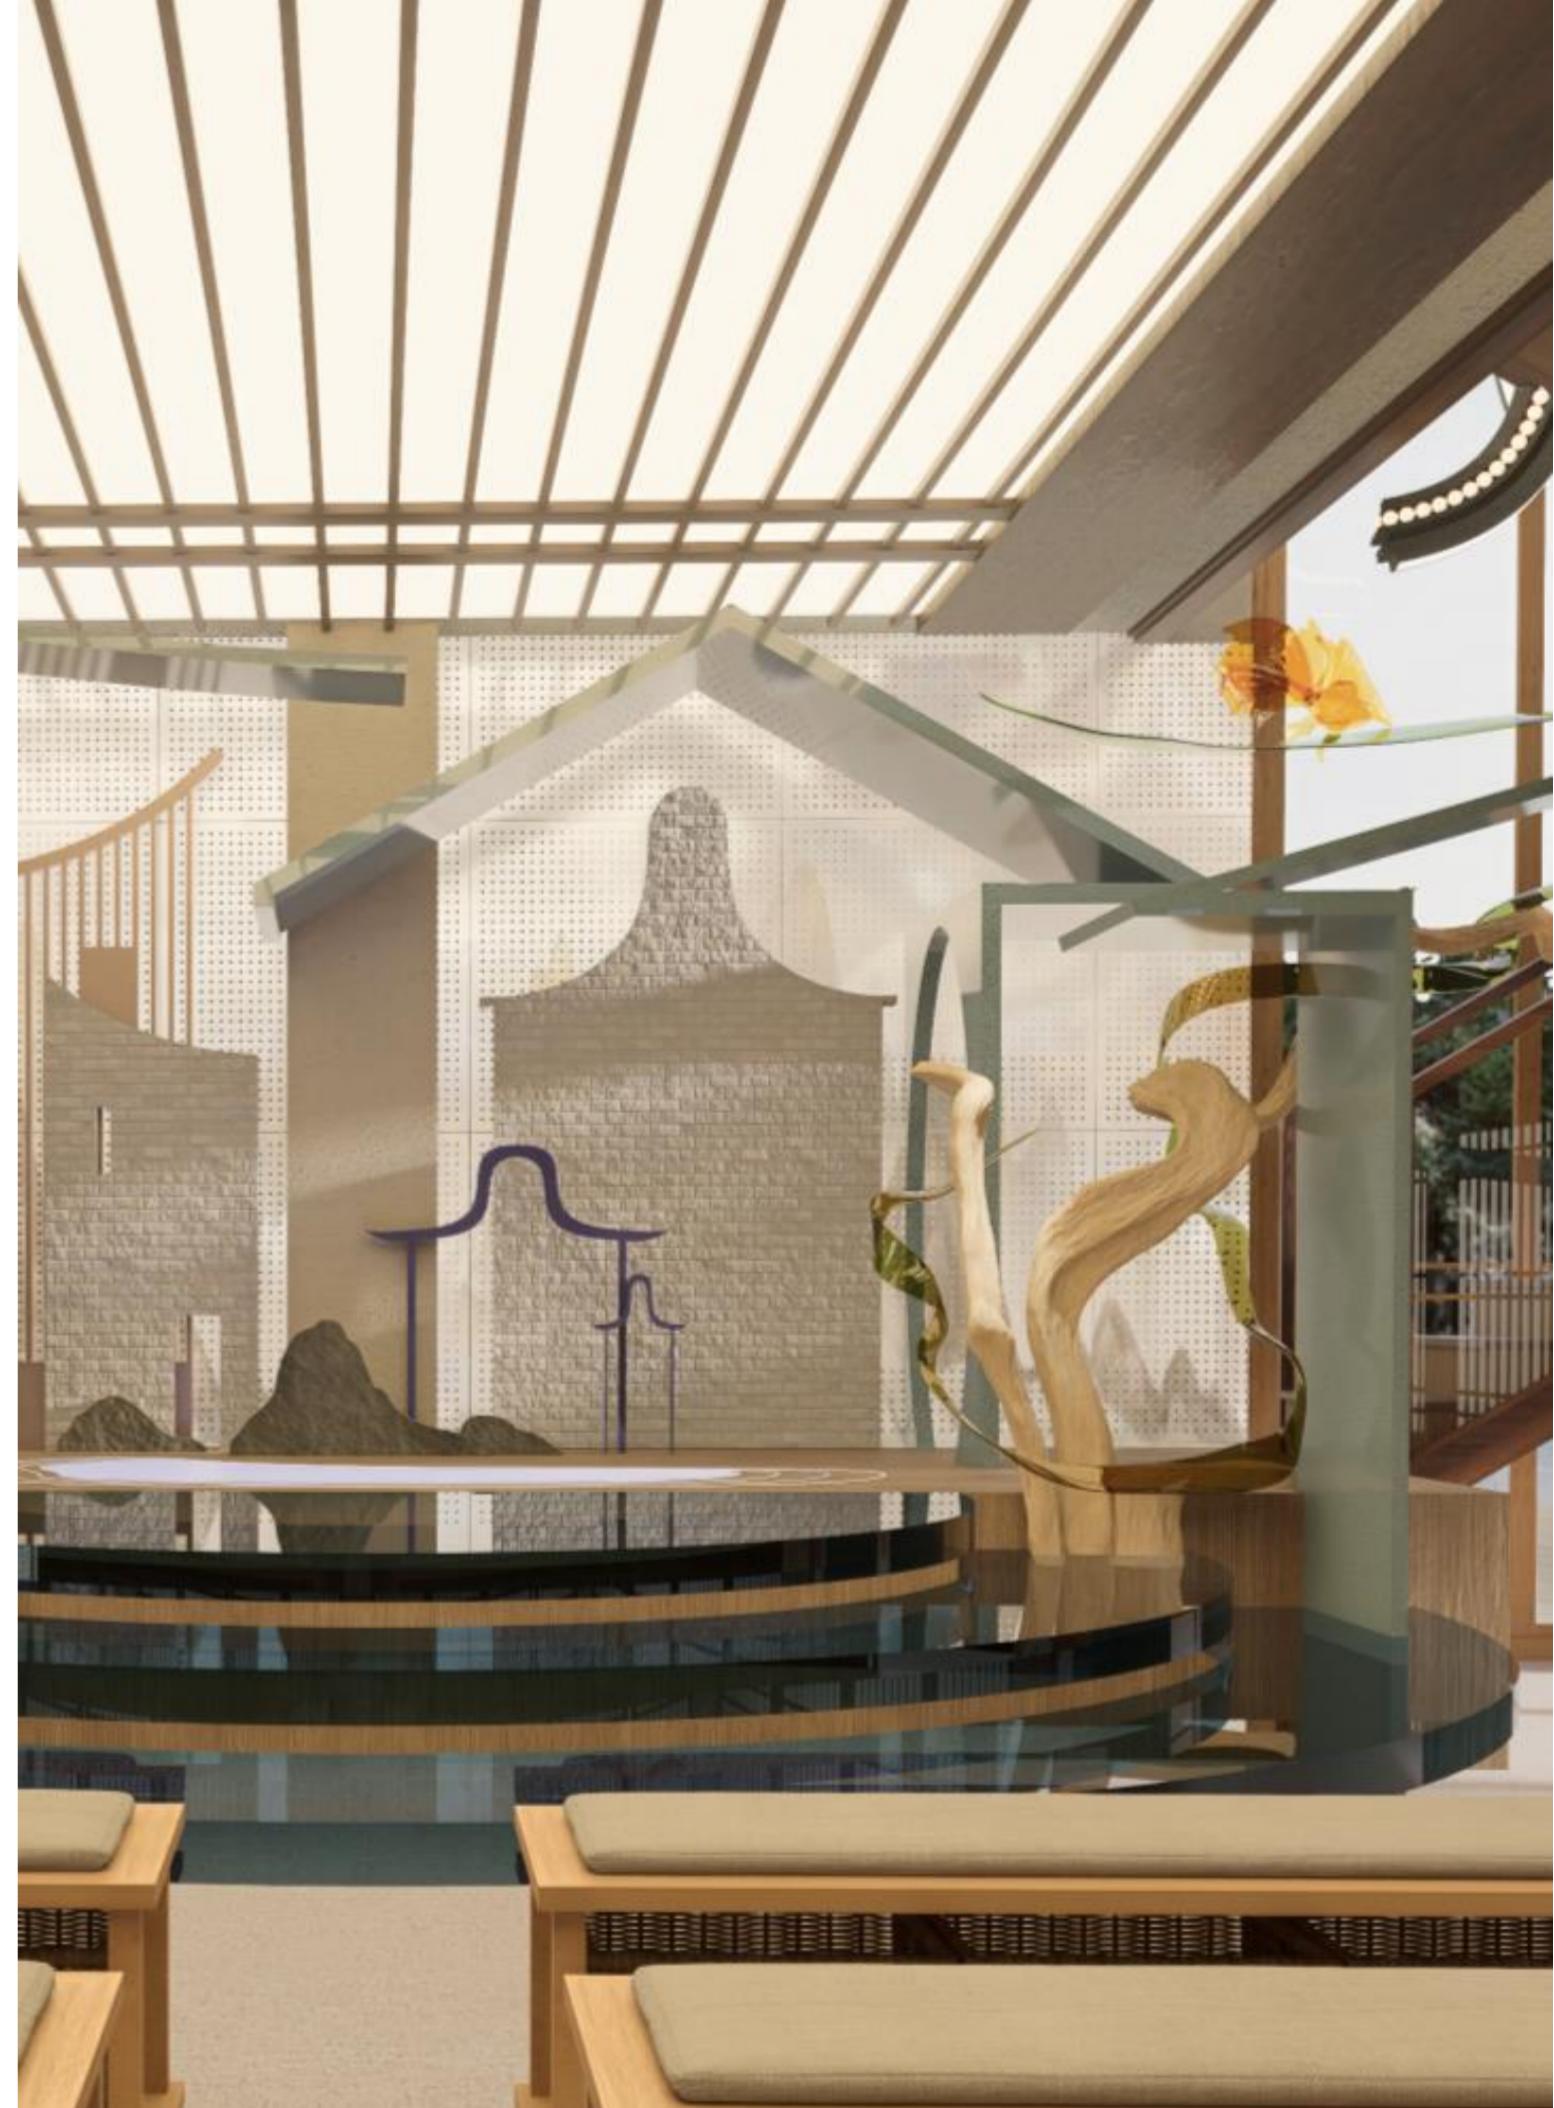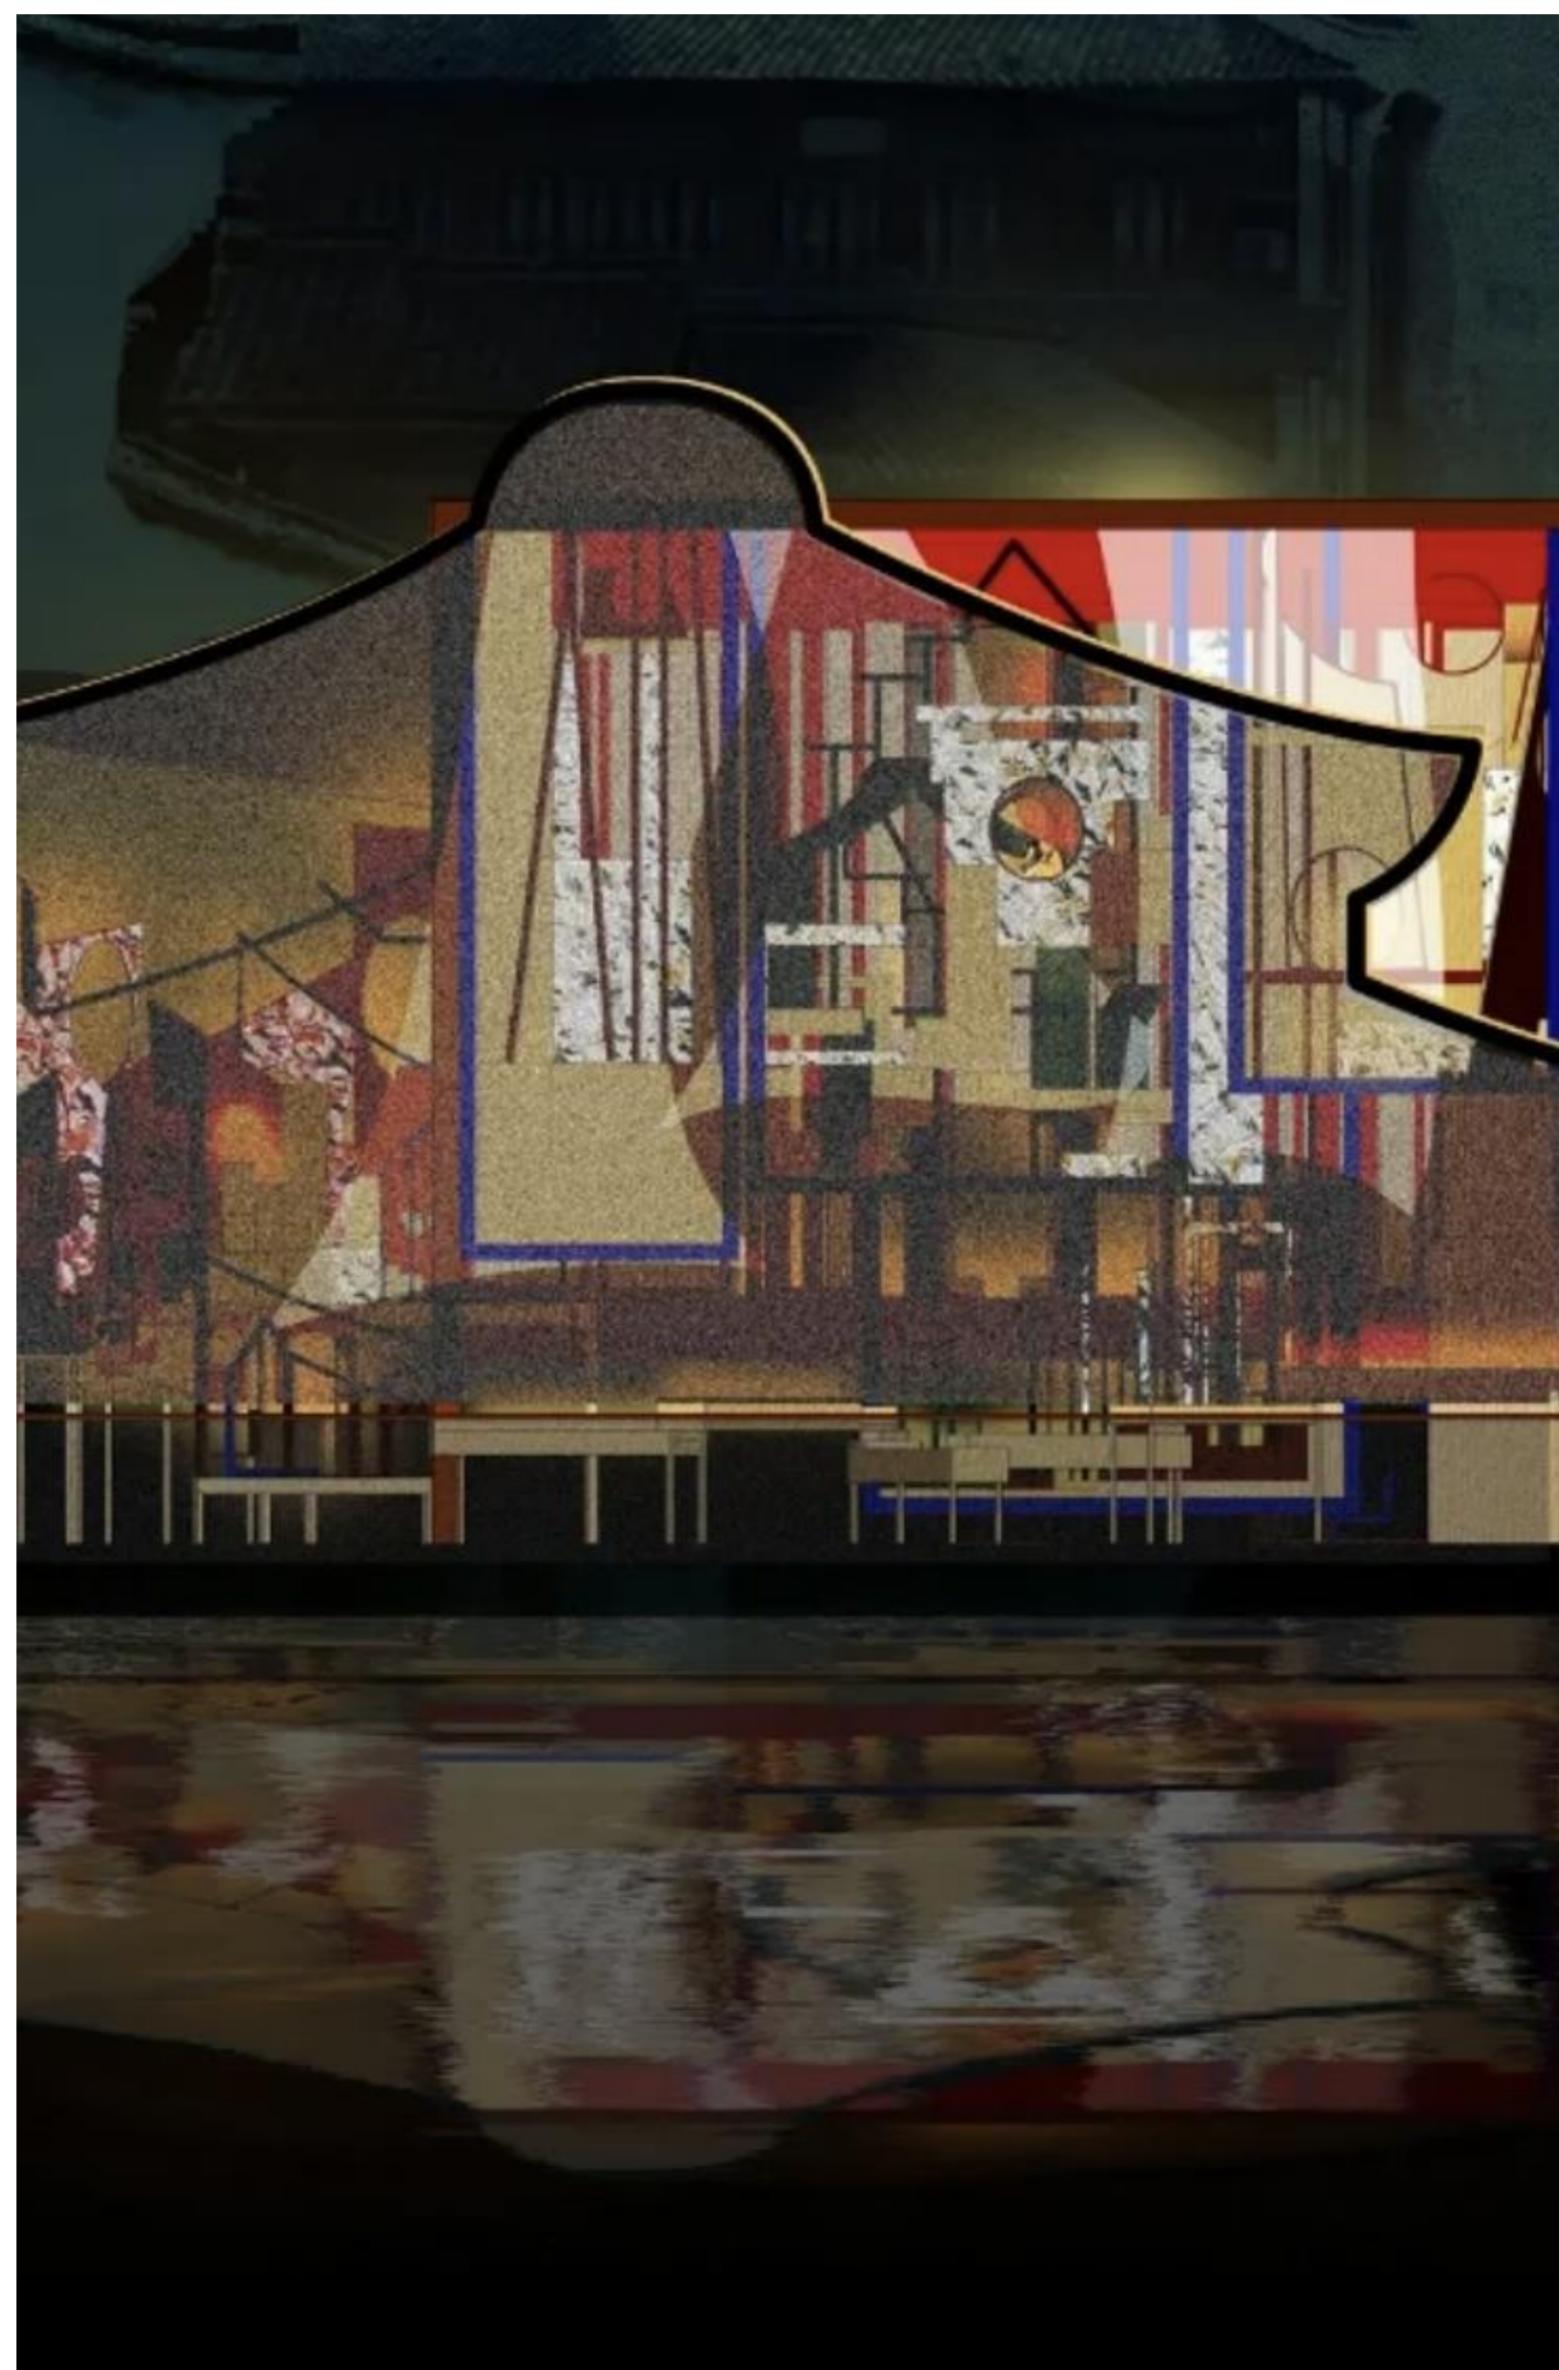

# 酒堂例規

A horizontal row of ten small black squares, evenly spaced, representing a sequence or a set of discrete items.



沿用酒堂本有的文化特色酒堂例规，将本来的场地安排与剧目时间结合，形成新的“酒堂例规”。



# 打卡体验

使用app获得完整酒堂文化浏览线体验，线上购票或购买餐饮节省排队时间。



售票亭处可兑换实体票  
根增强旅行体验感。



# 材质表现

.....

3B3837

B5AFAF

643029

F0D1A1

98654A

A6BE86




樱桃木

白桦木

青石板

仿古地砖

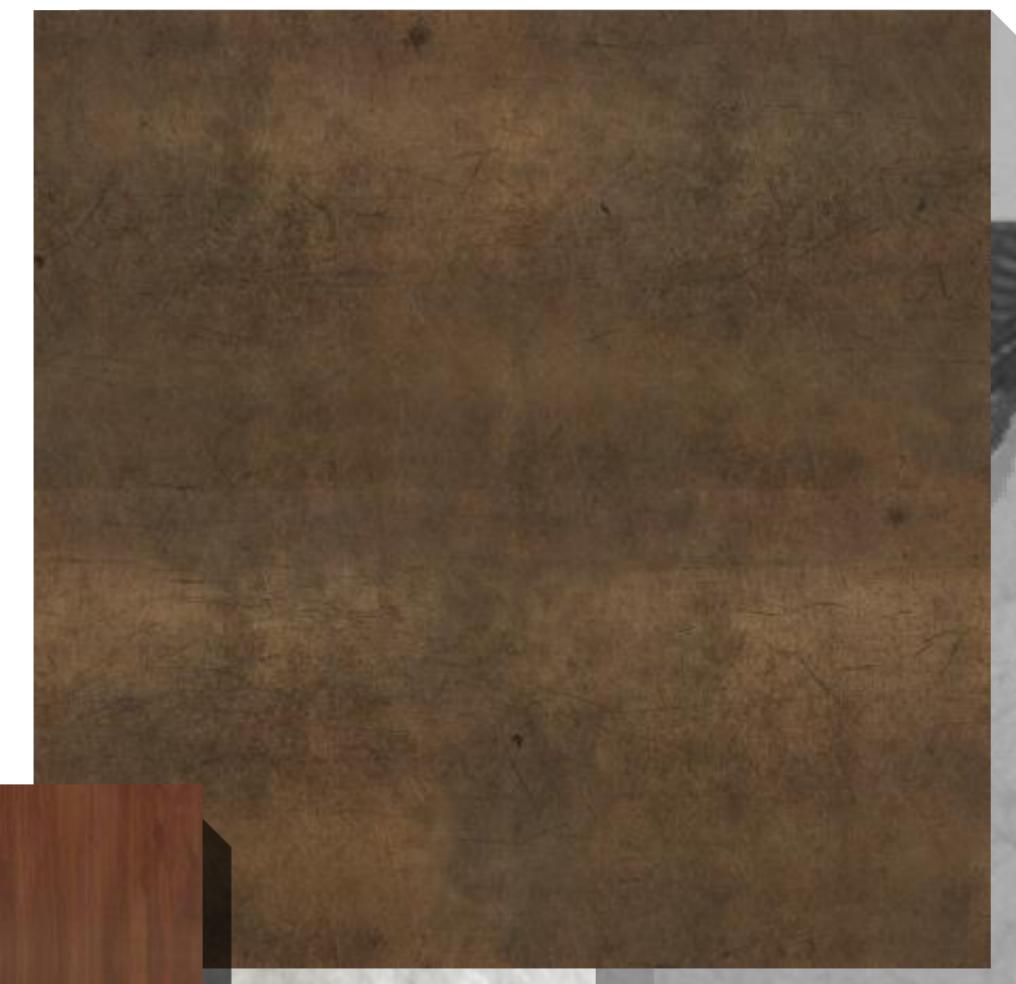

瓦片



# 设计方案

· · · · ·

传统剧院 · 剧场 · 饮品店 · 茶室

# 爆炸图



# 设计方案



总平面 1:500

# 设计方案




南立面

# 设计方案




东立面

# 设计方案

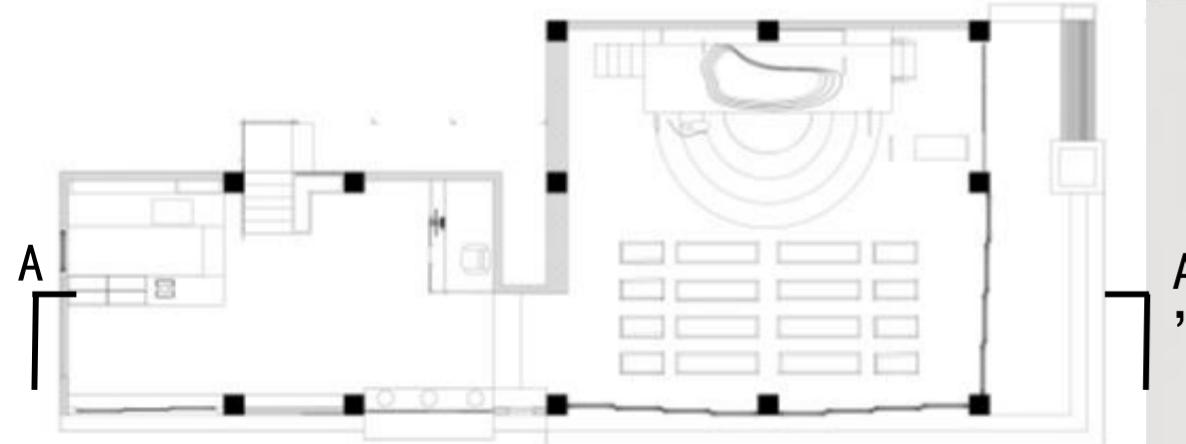


A-A'剖面图


# 设计方案

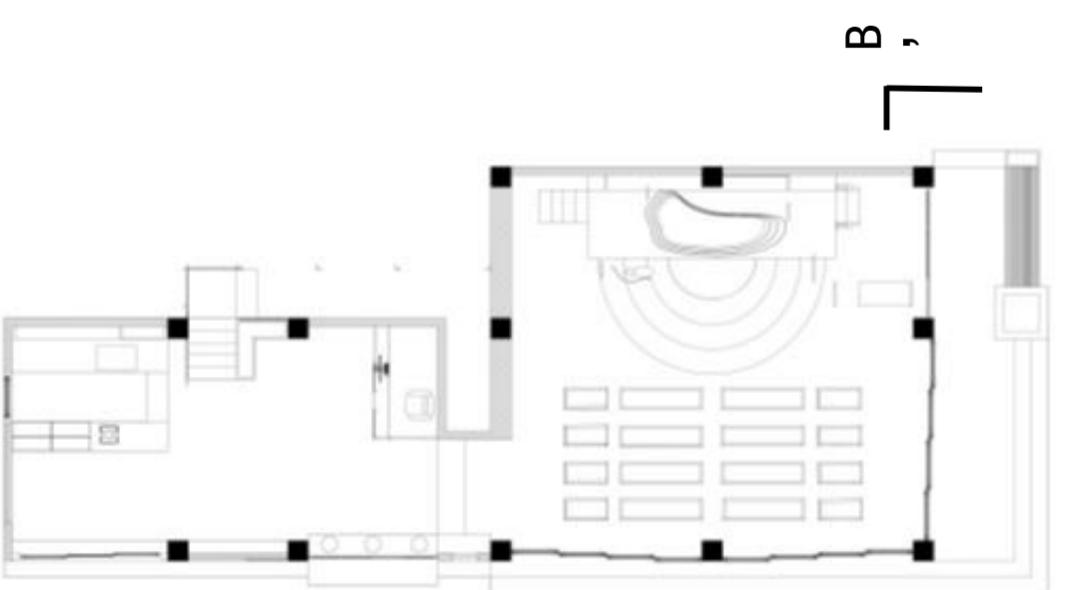

B-B'剖面图

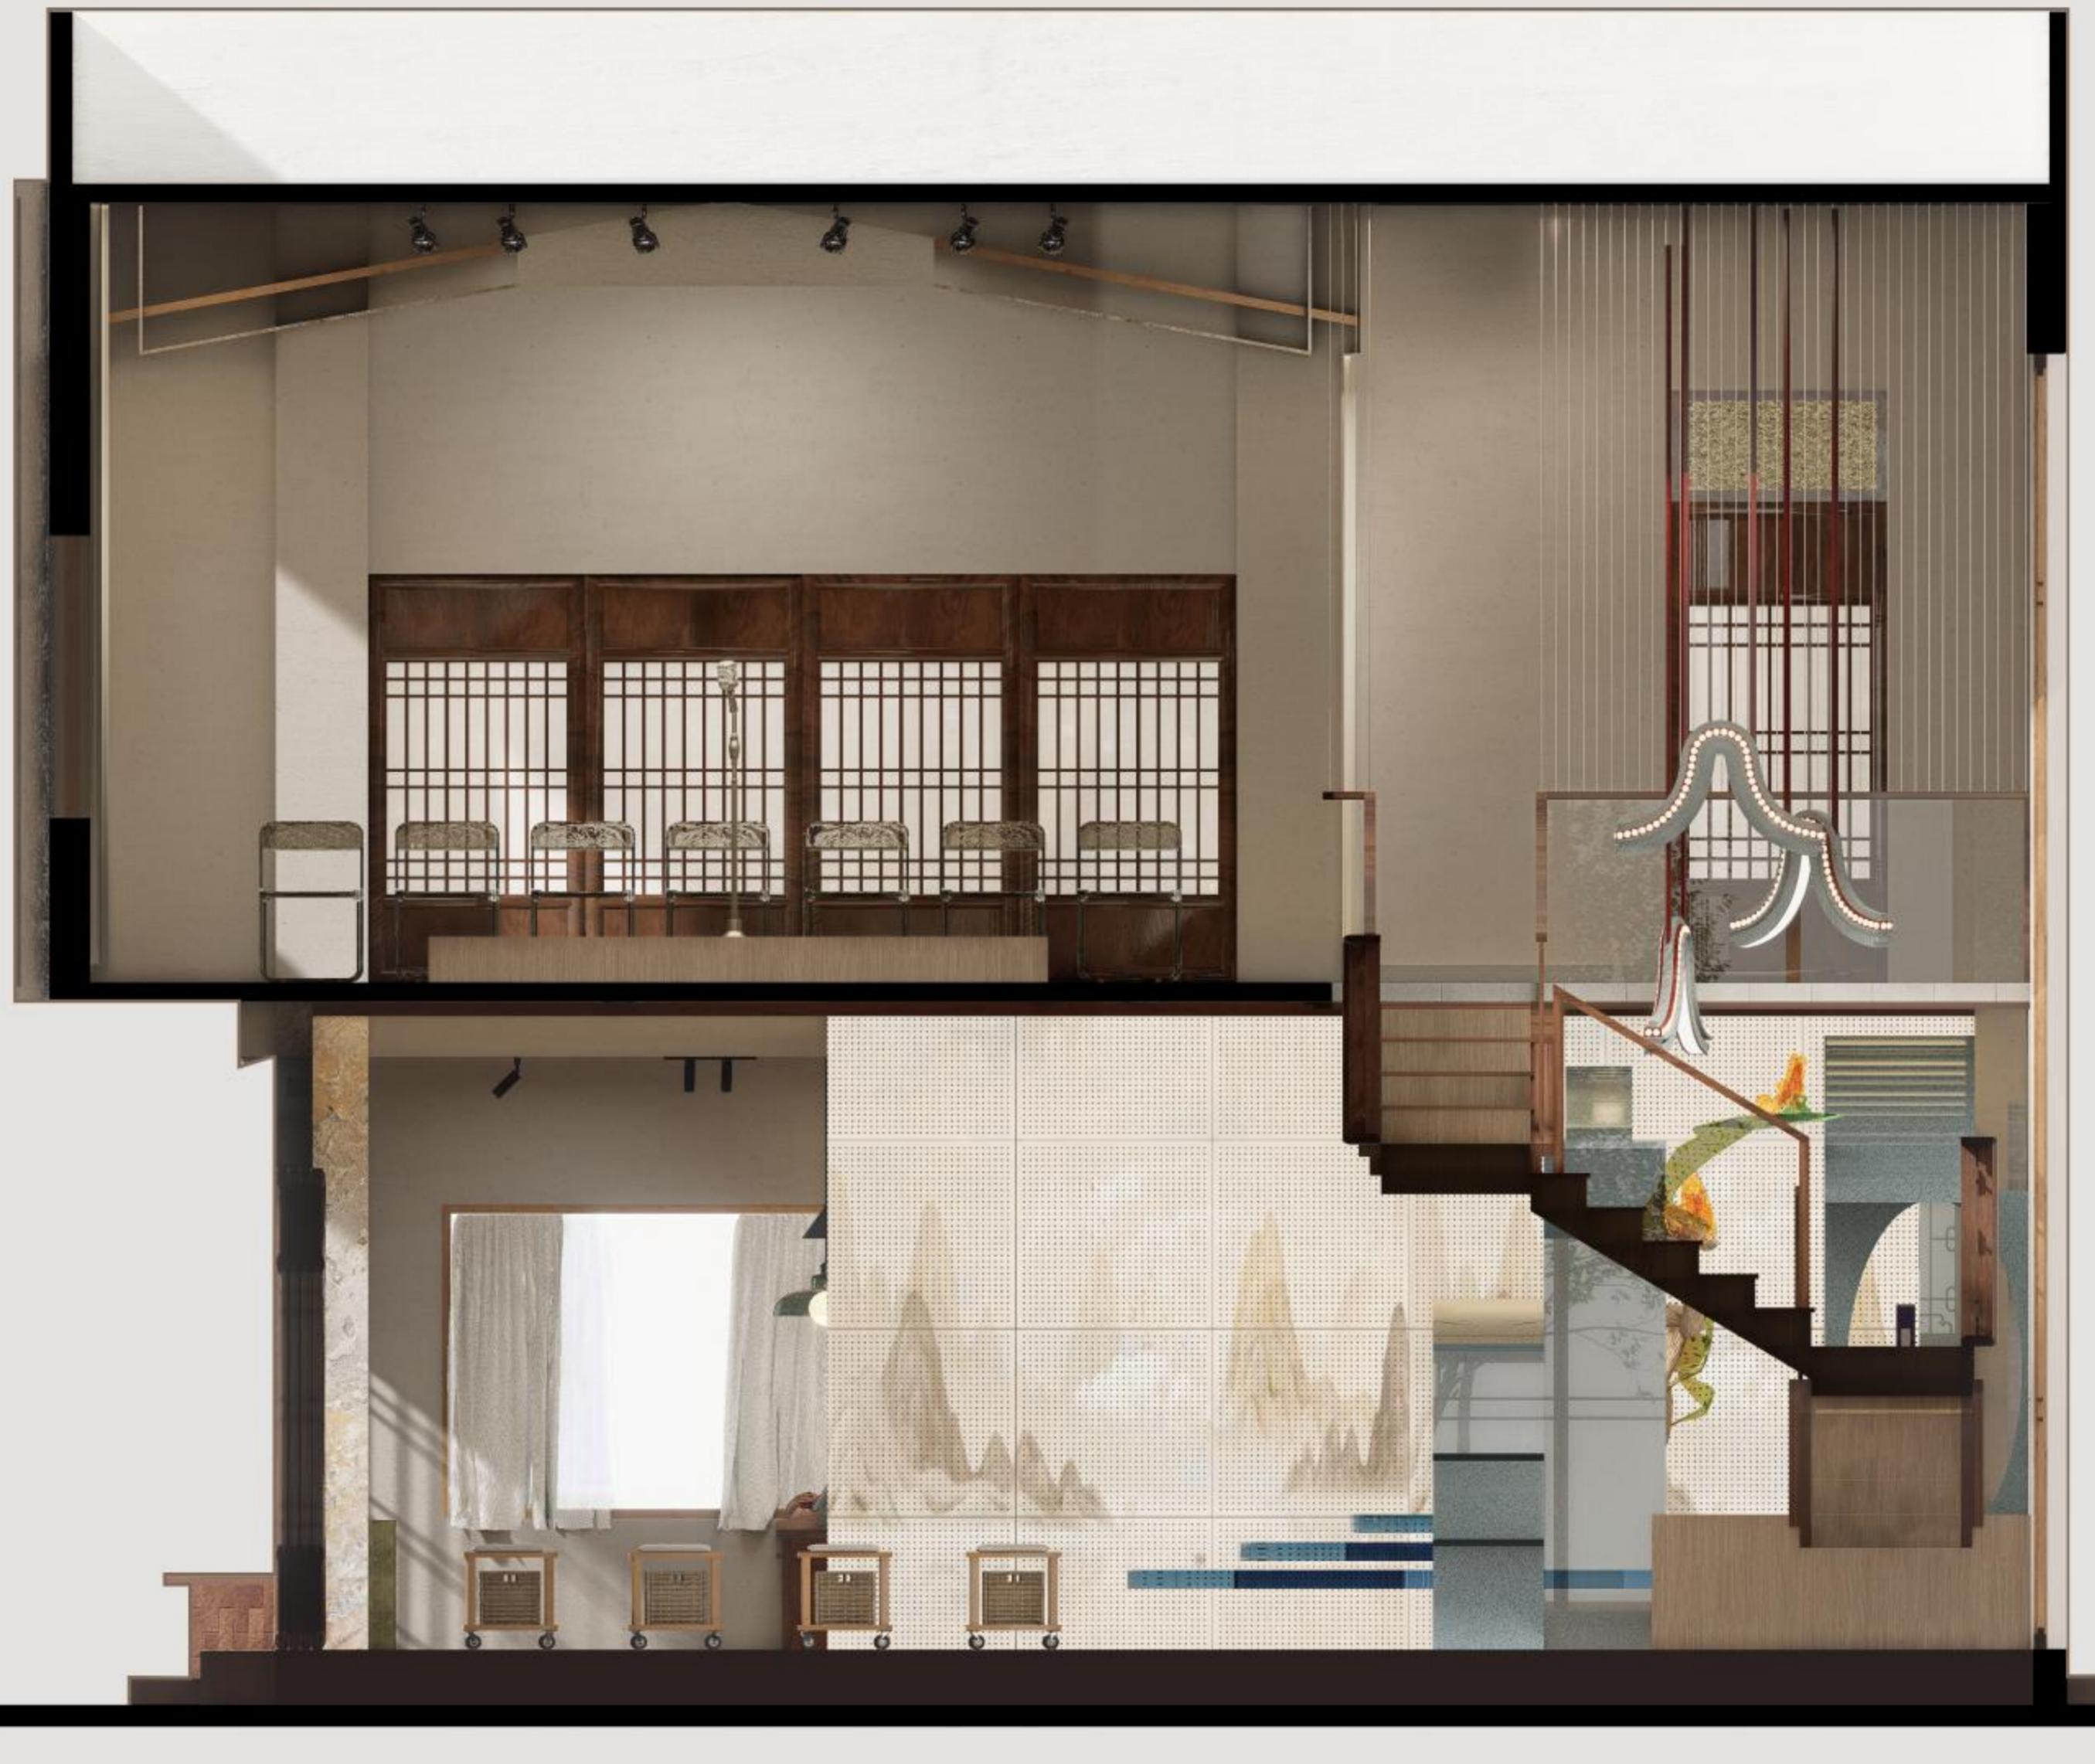

## 设计方案

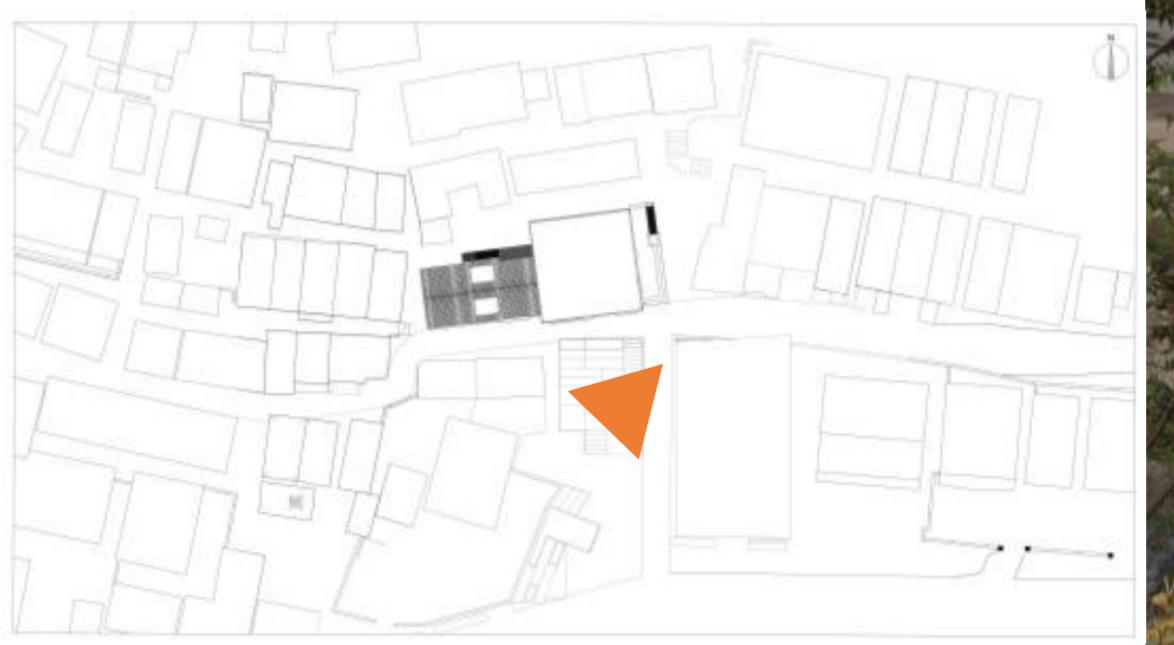

室外公共空间效果图



## 设计方案



室外公共空间效果图



## 设计方案



室外公共空间效果图

## 设计方案

剧场围合的状态效果图




## 设计方案

剧场开放的状态效果图



# 设计方案

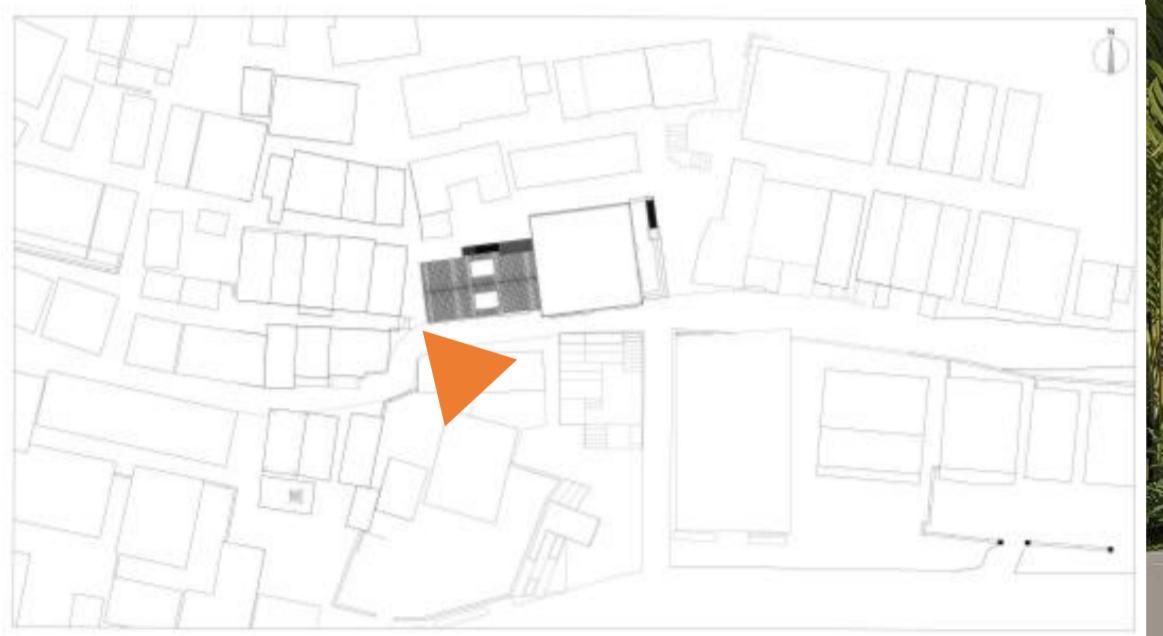

茶饮店室外效果图




# 设计方案




一楼平面图

# 设计方案

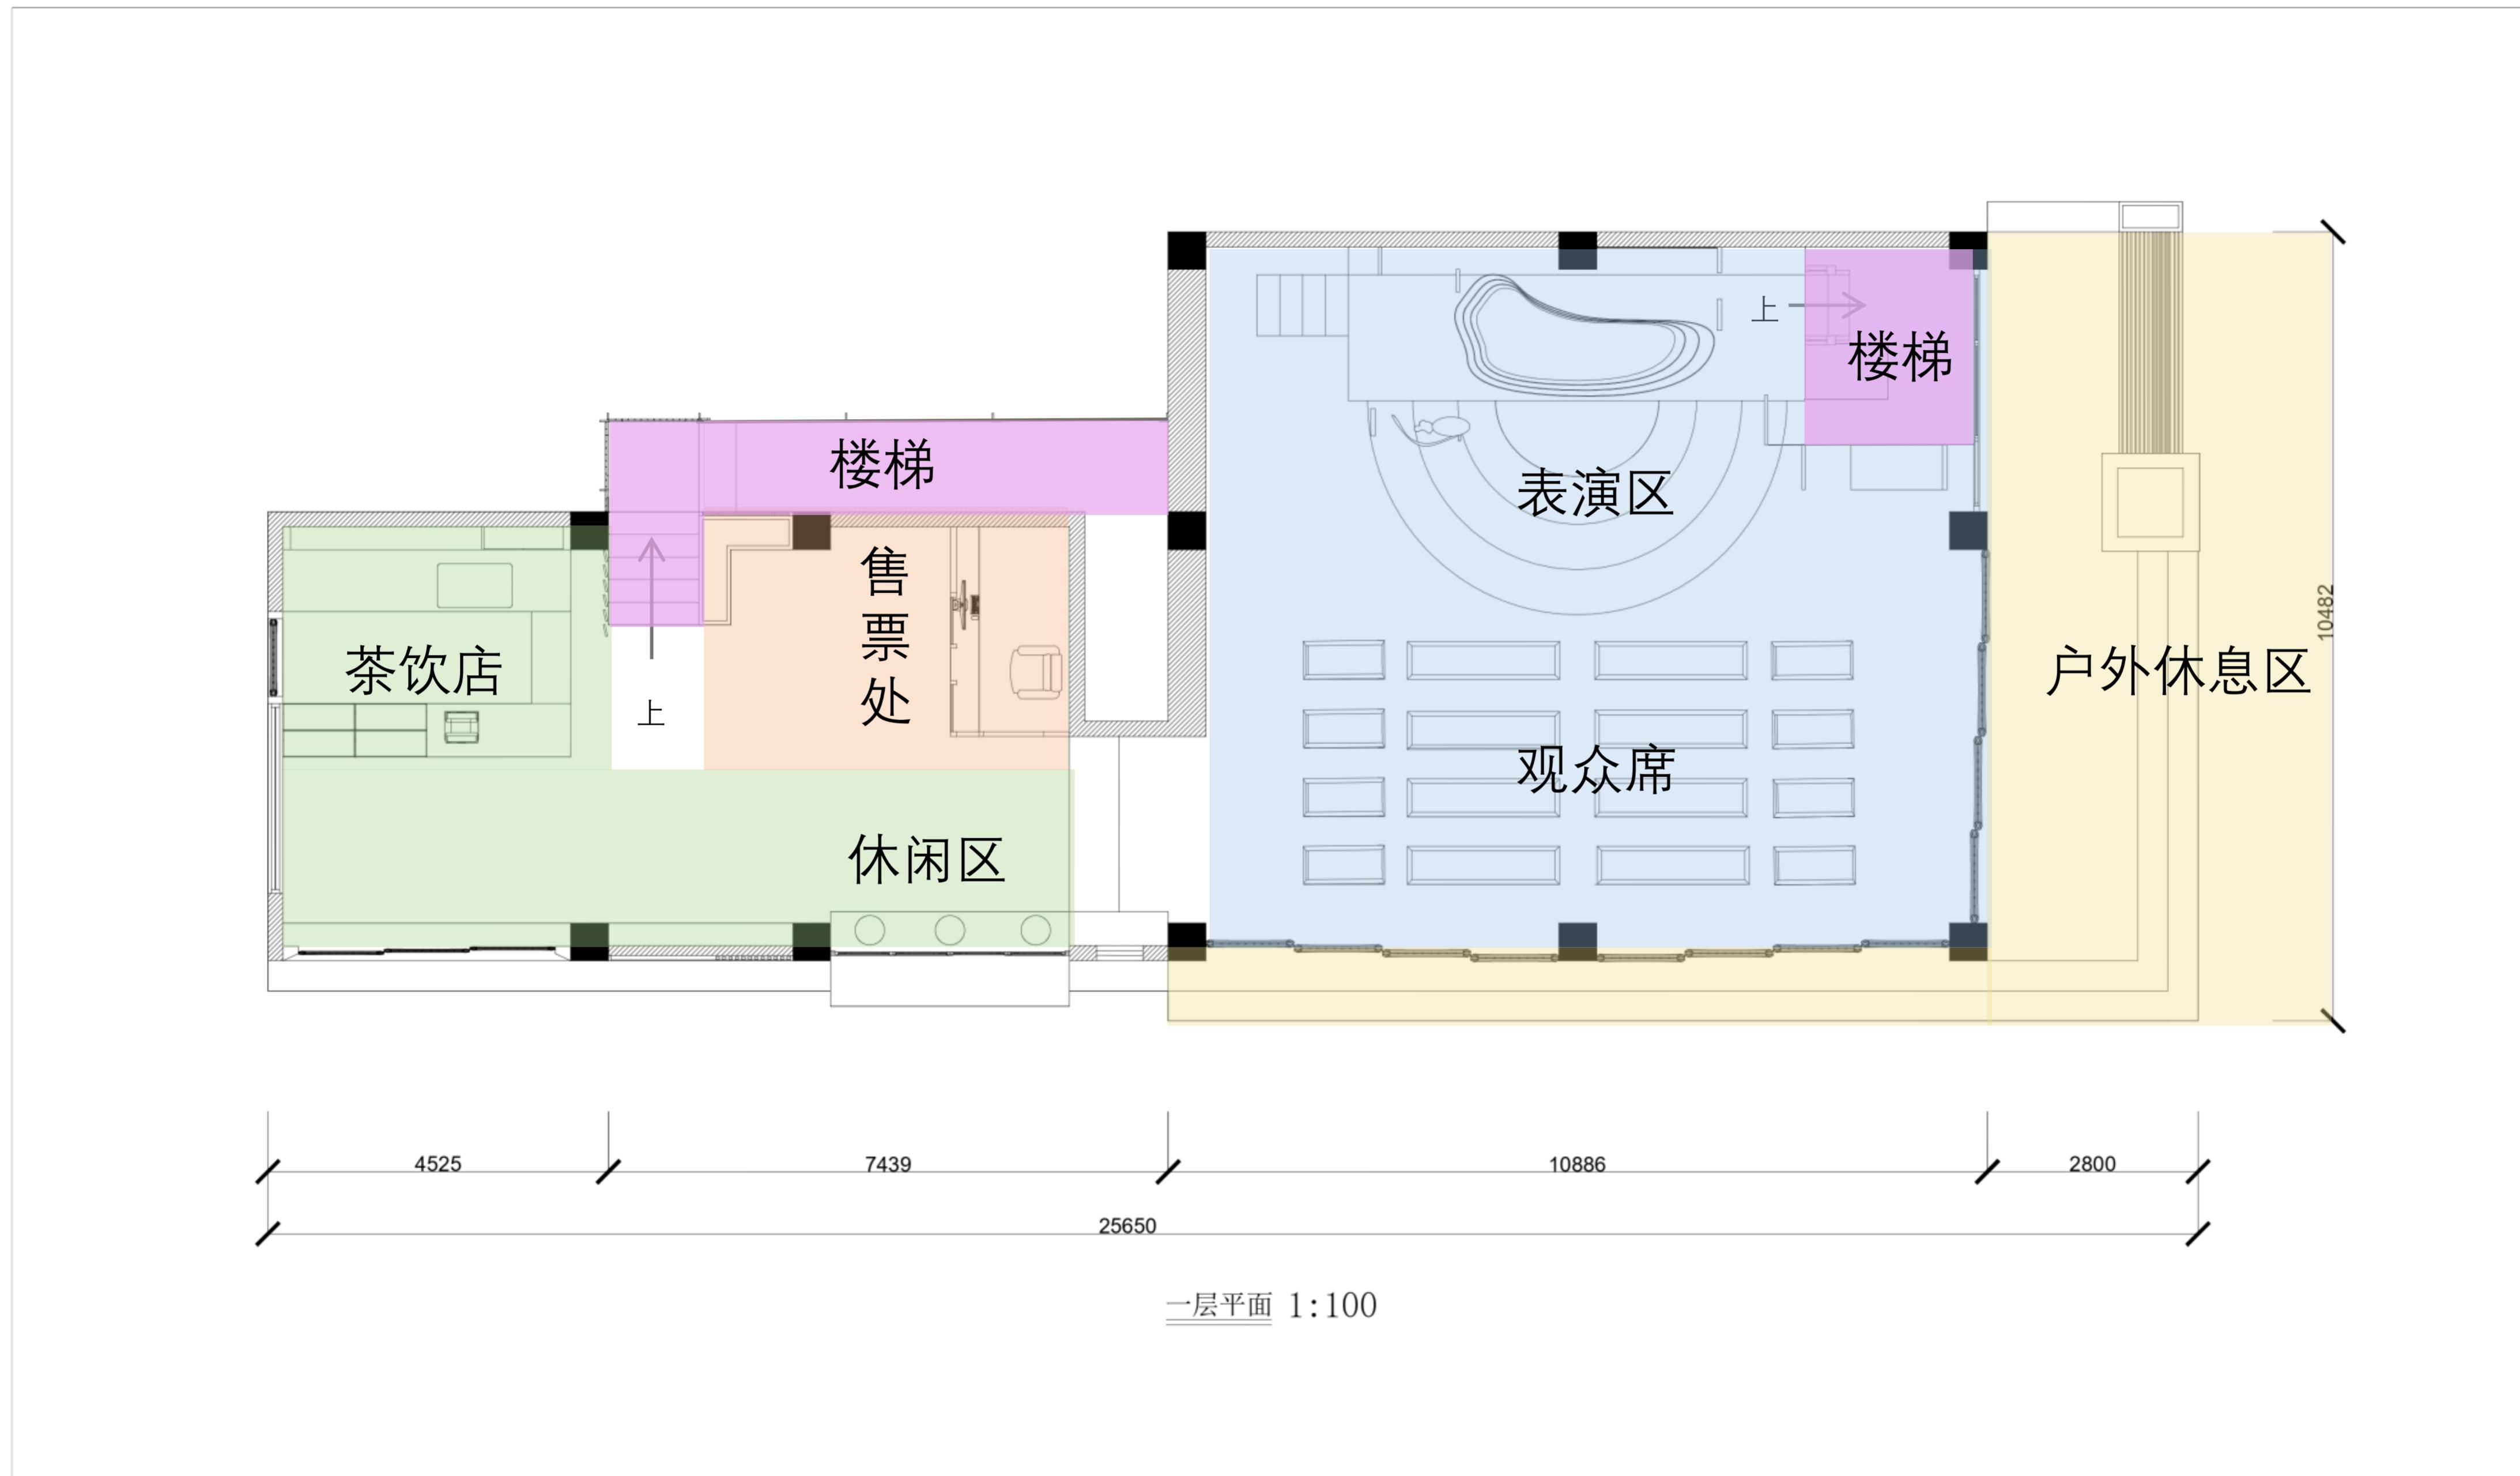

一楼功能分区

# 设计方案

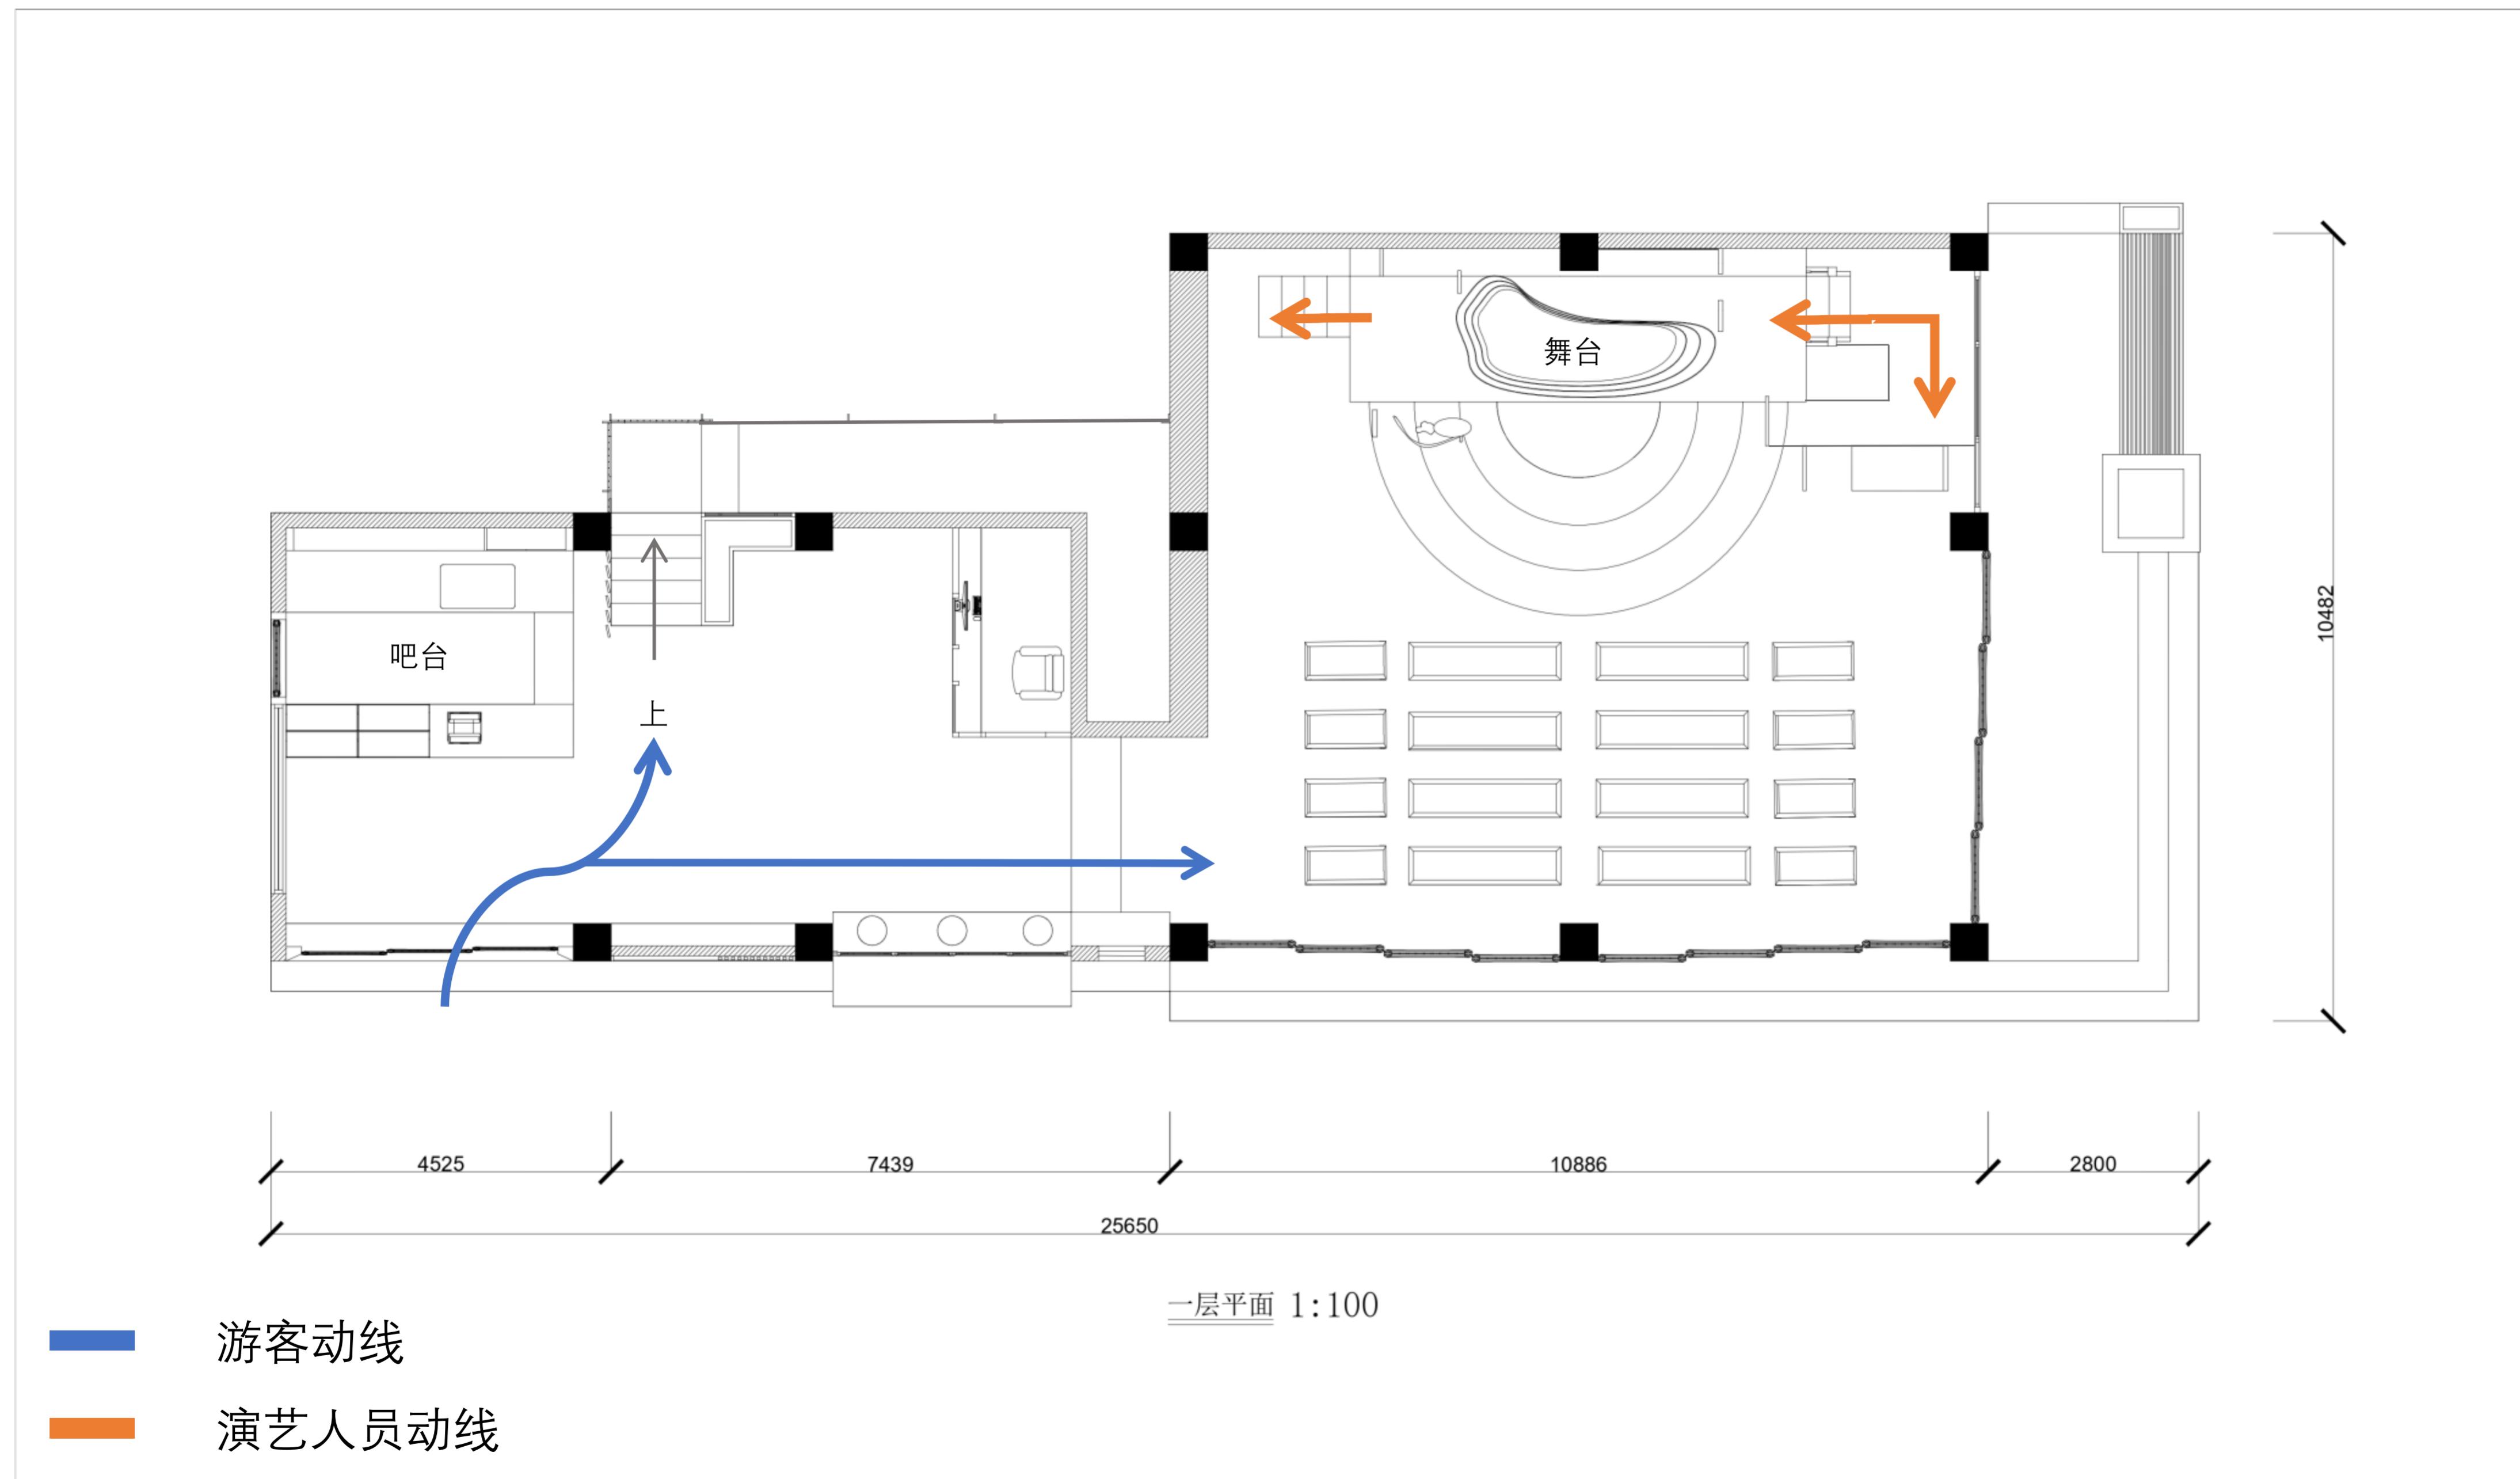


一楼动线图

# 设计方案



茶饮店效果图


# 设计方案

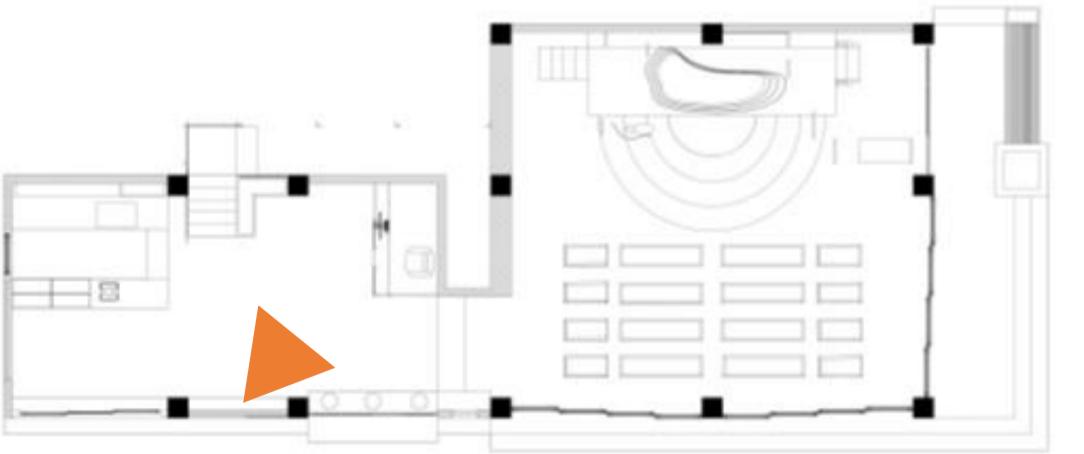

售票亭效果图




## 设计方案

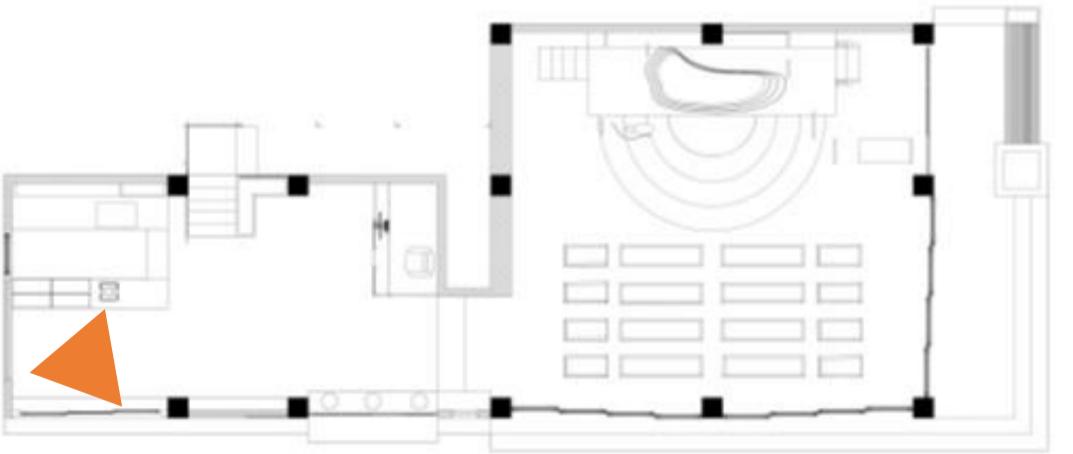

休闲区效果图




## 设计方案

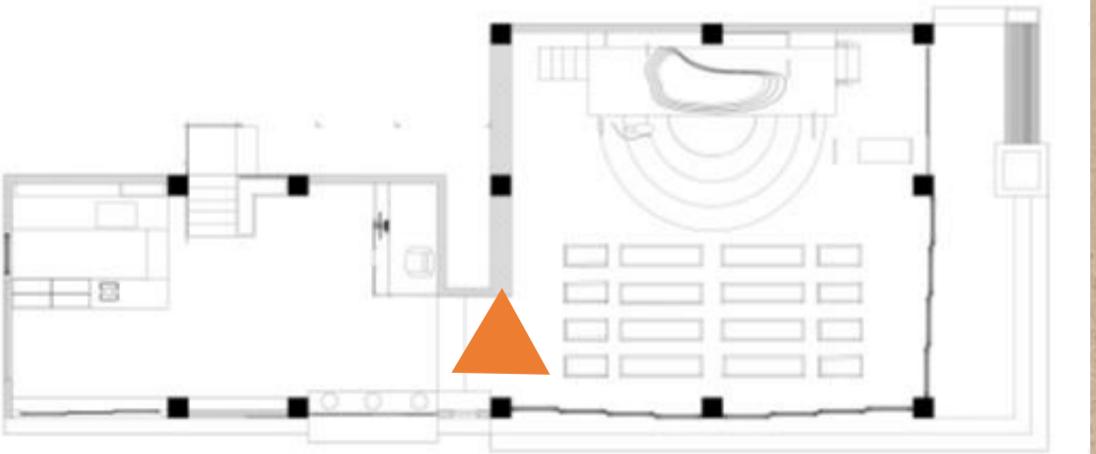

剧场效果图



## 设计方案

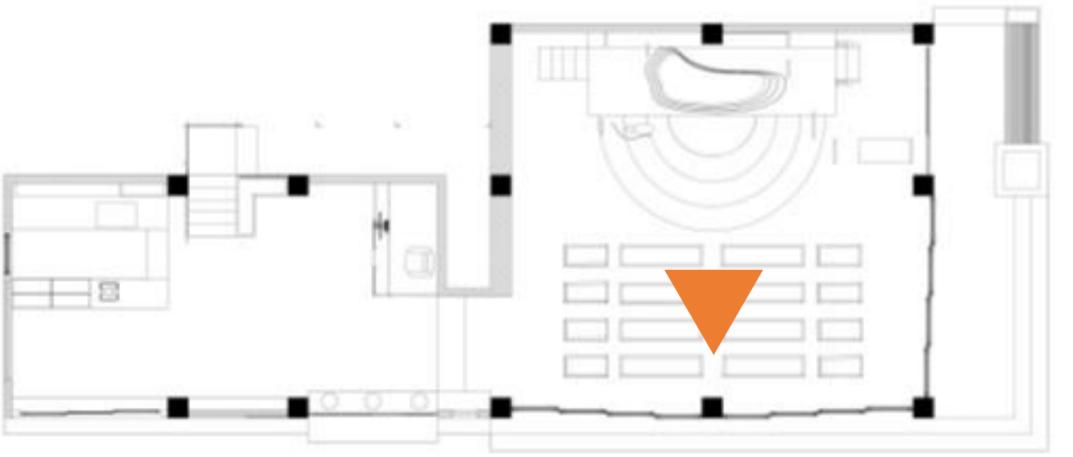

剧场效果图





表演效果

表演效果




# 设计方案




二楼平面图

# 设计方案

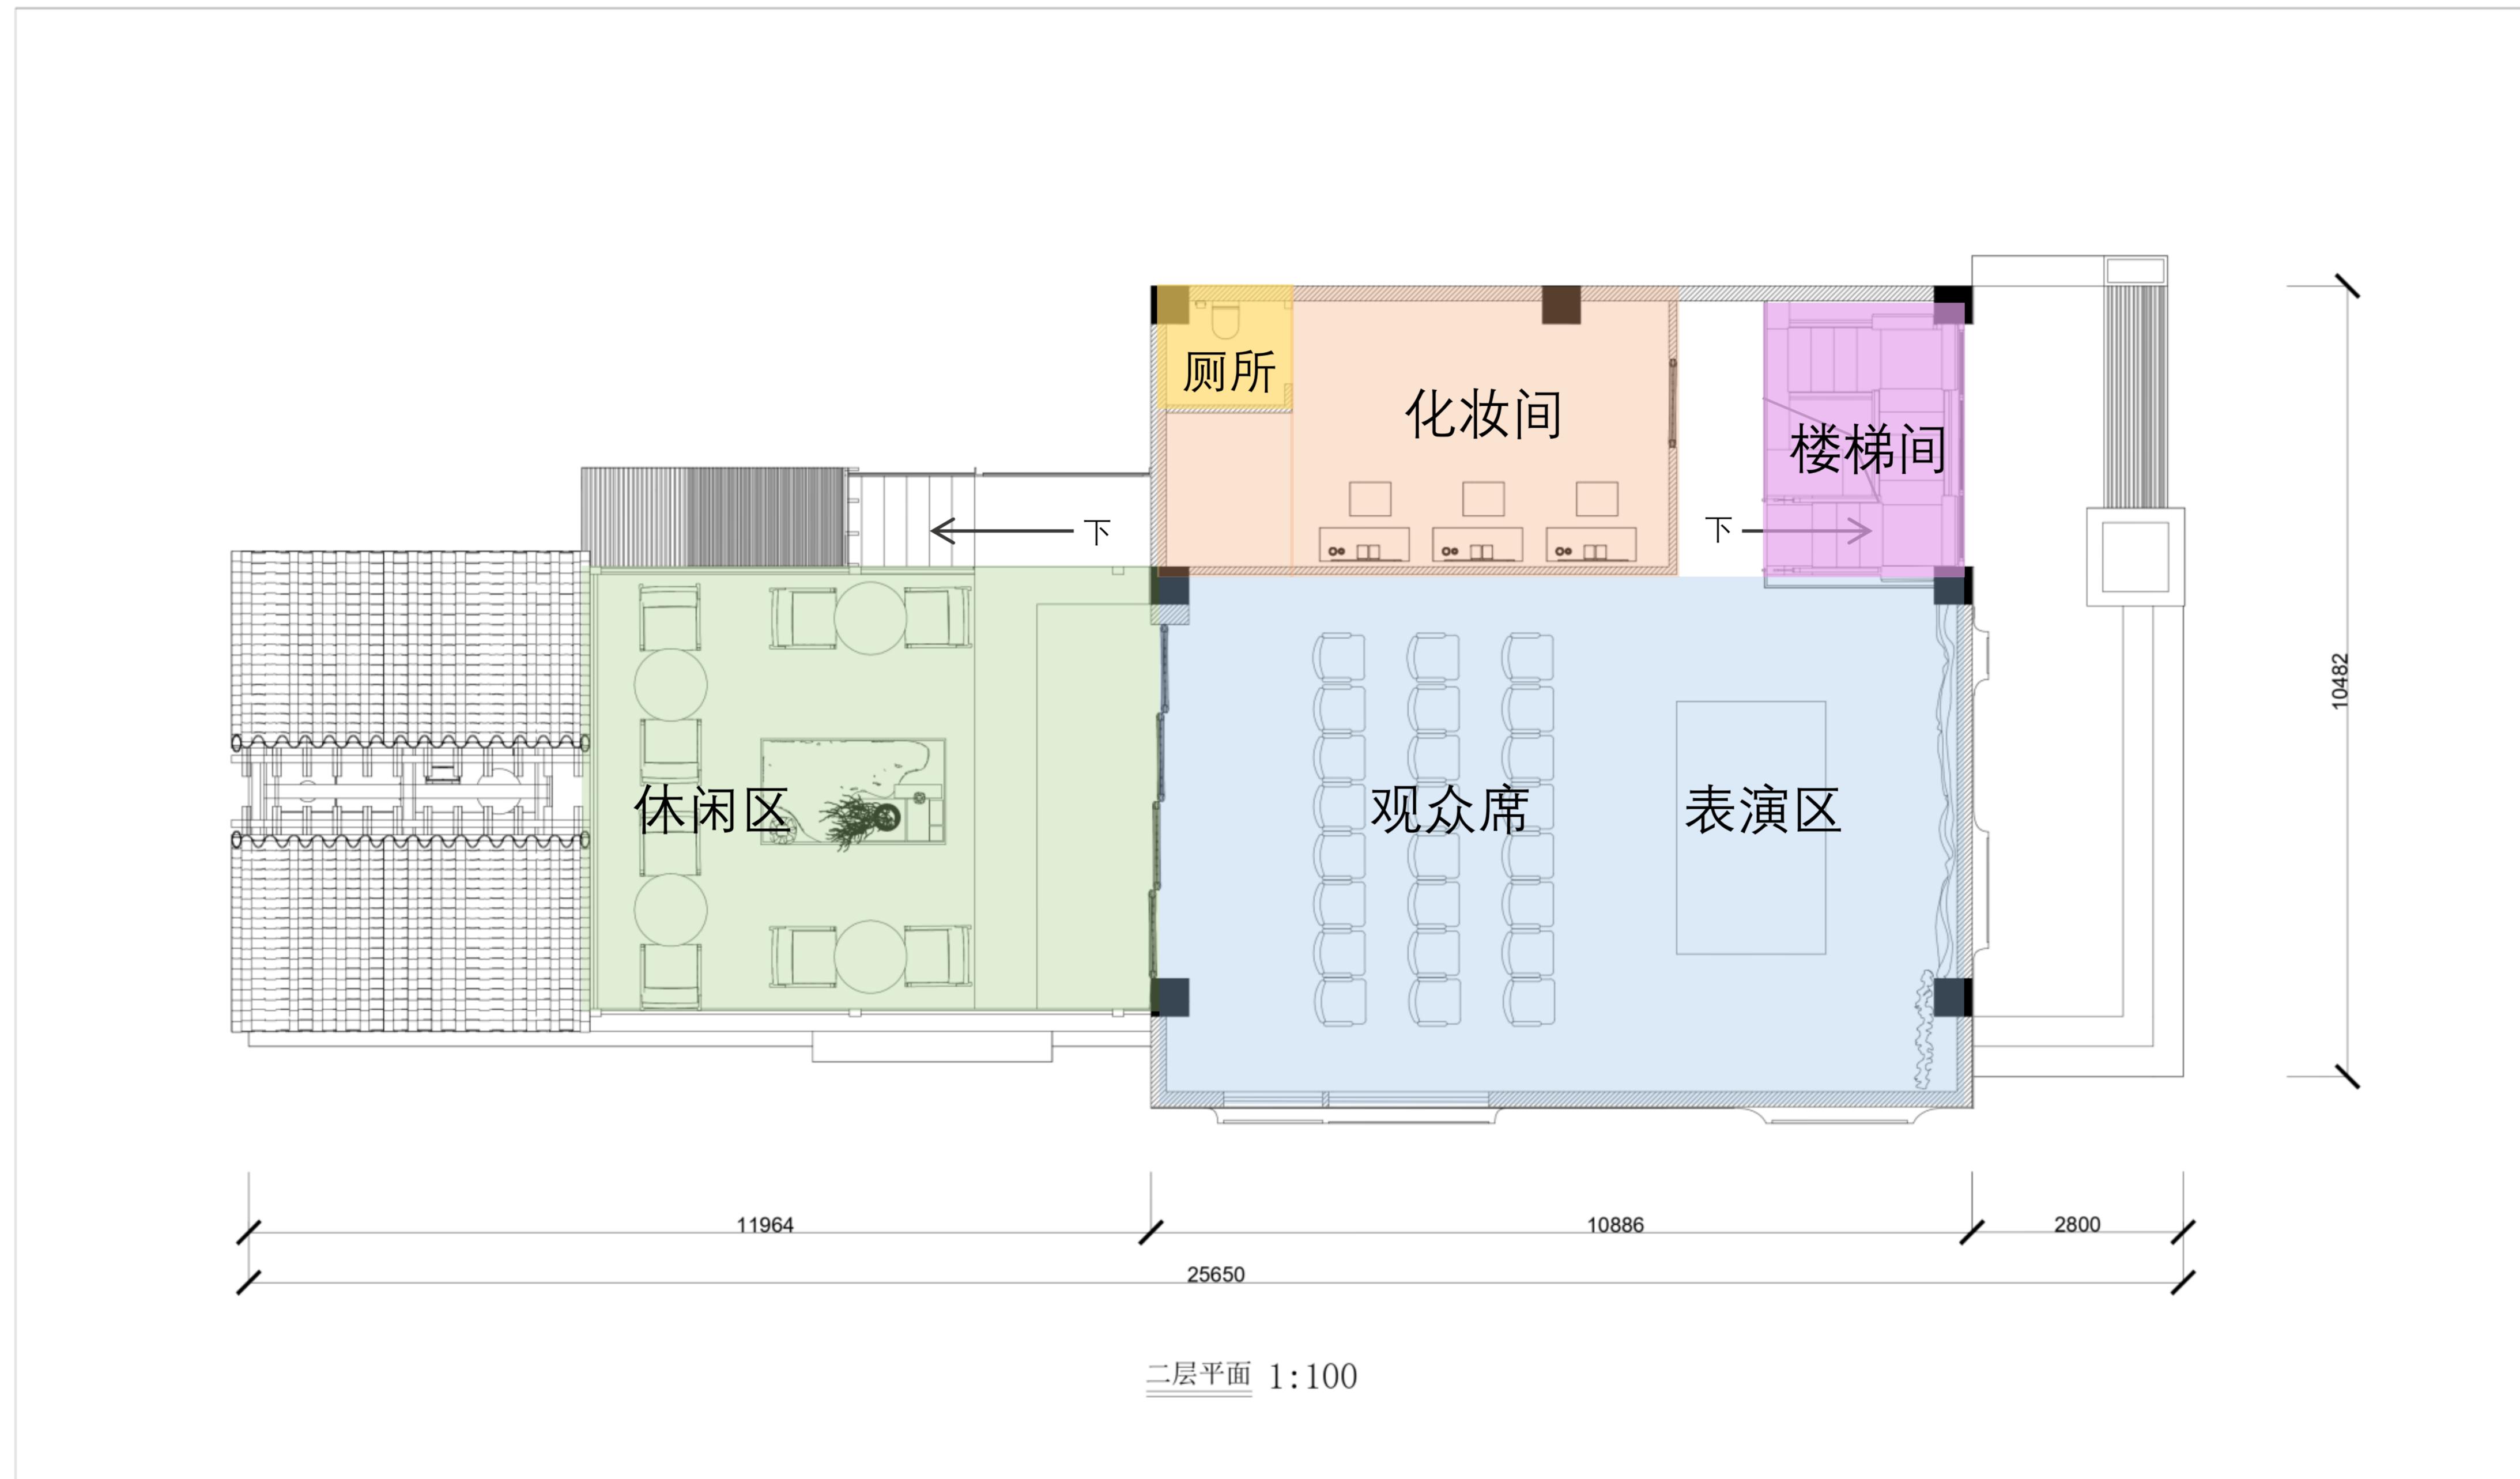

二楼功能分区图

# 设计方案

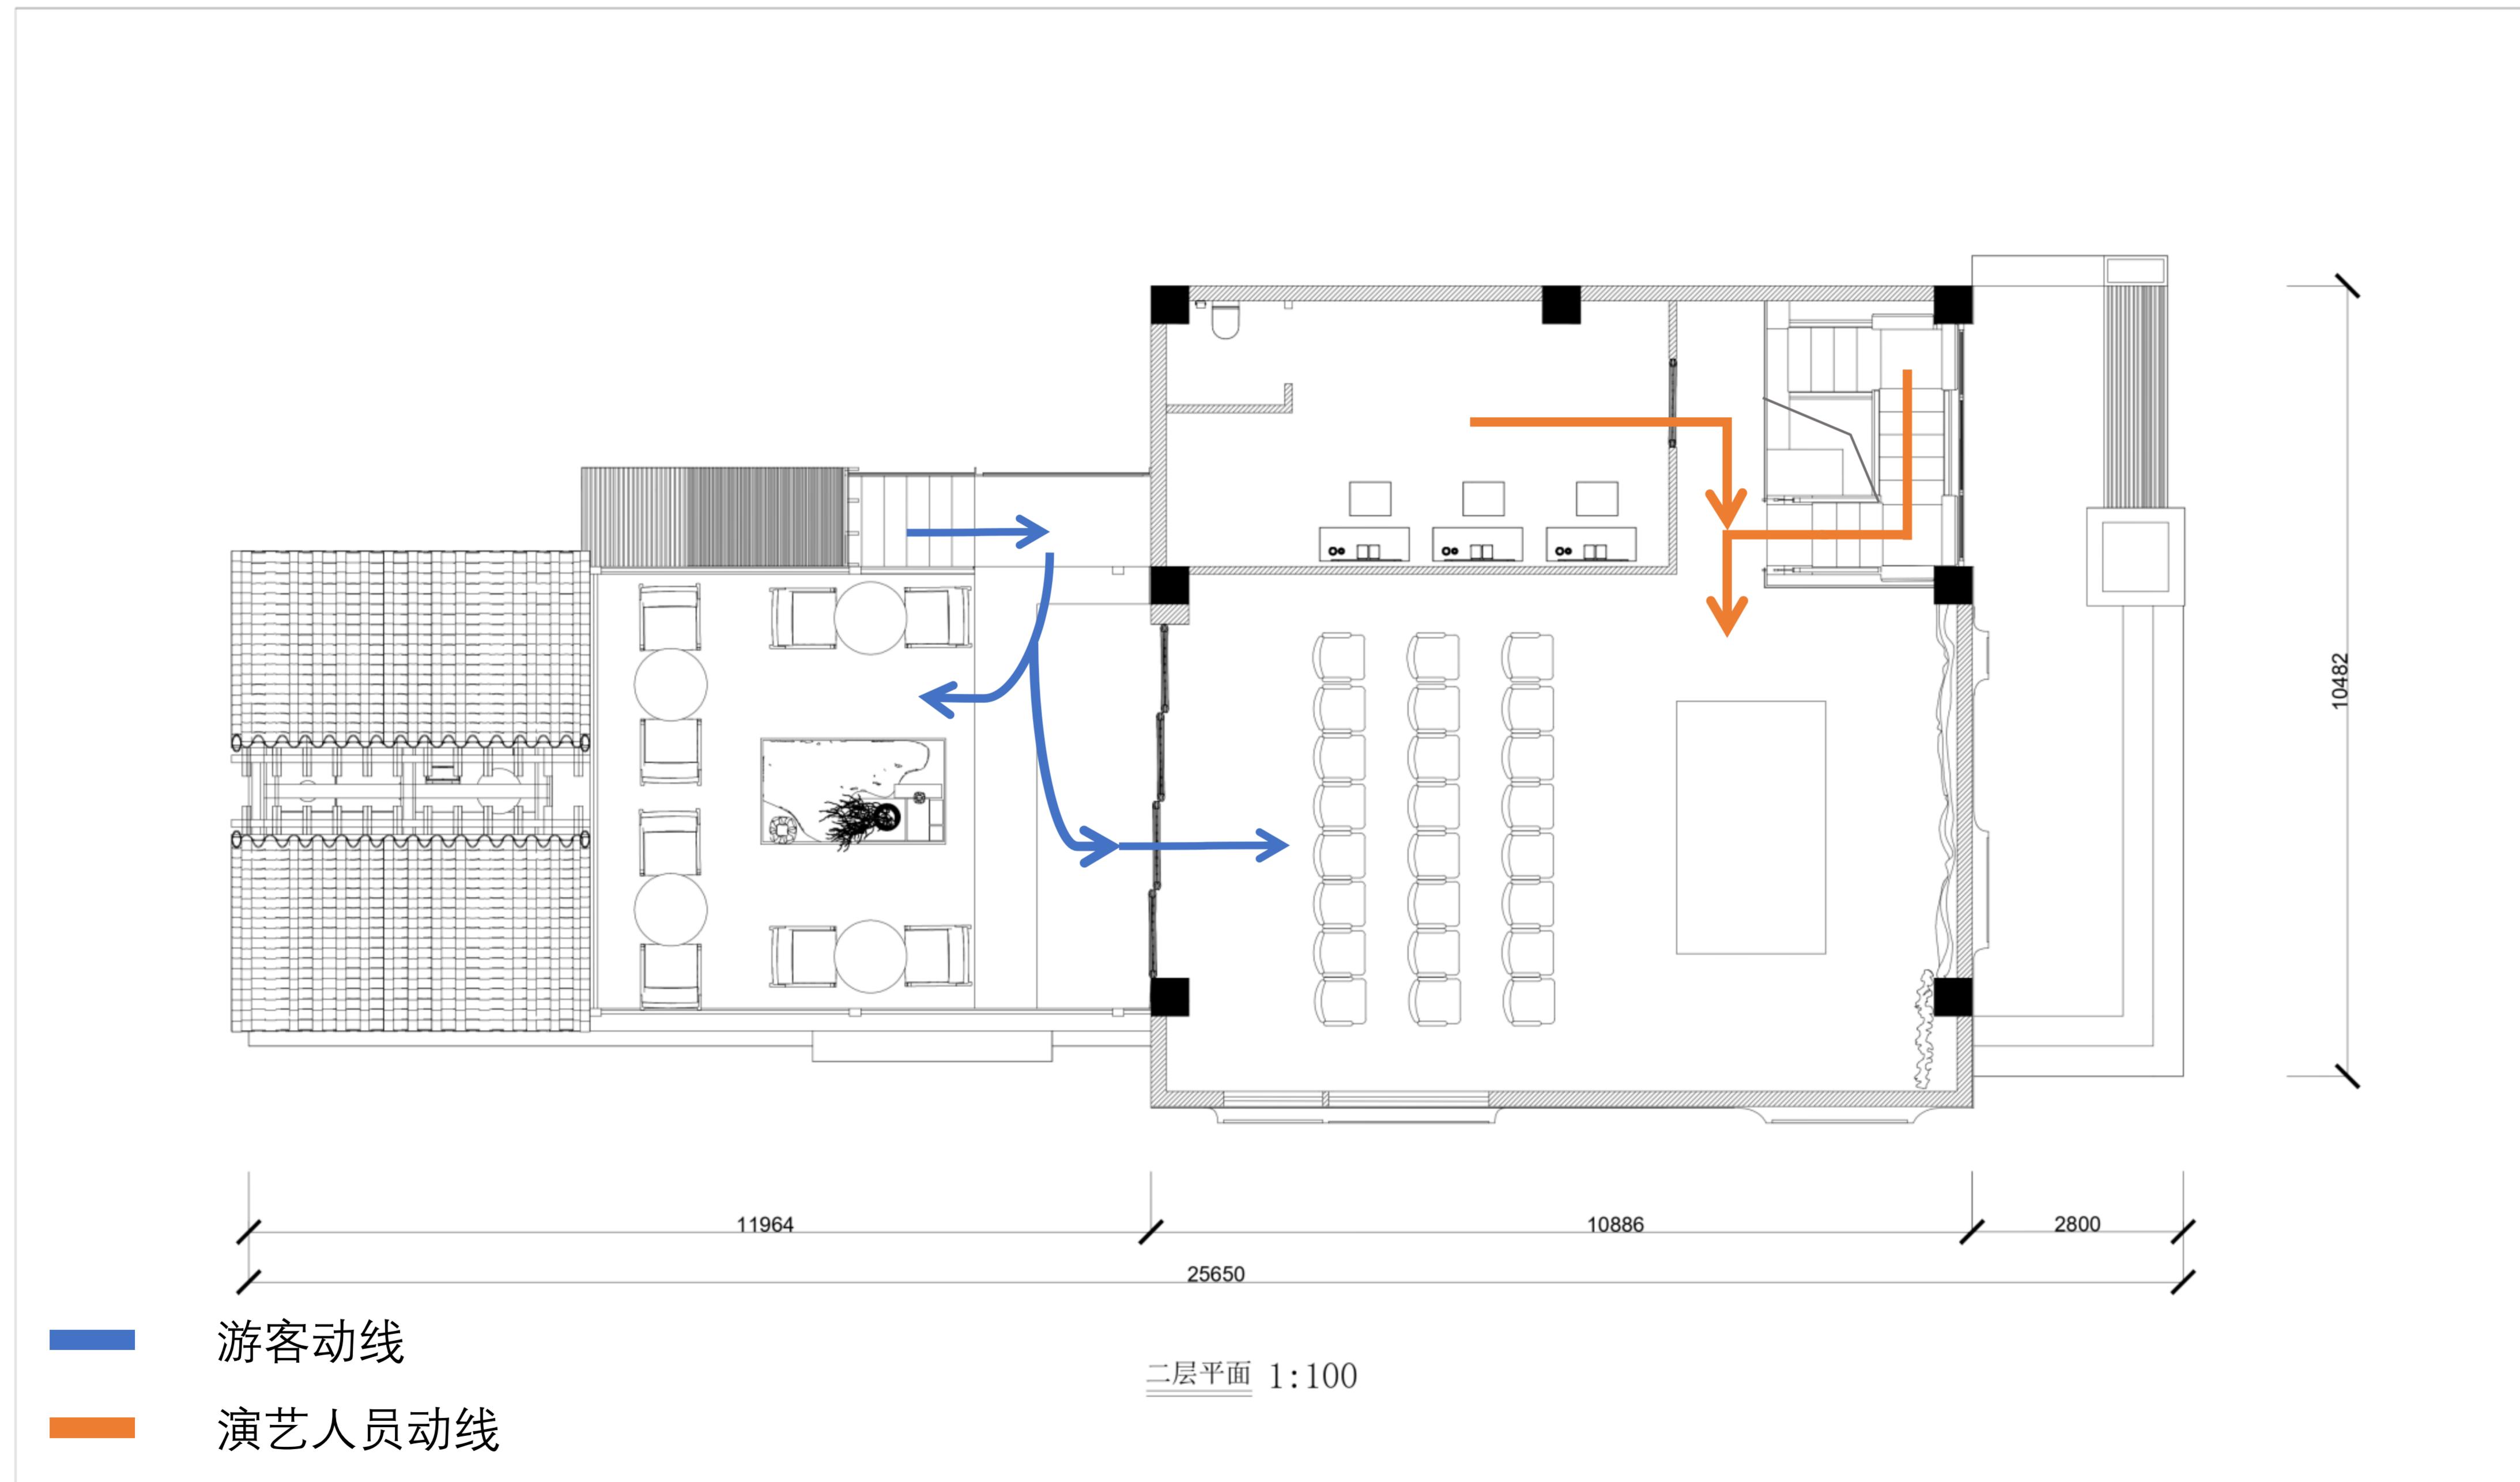

二楼动线图

# 设计方案



楼梯效果图



## 设计方案



休闲区效果图




## 设计方案



休闲区效果图



## 设计方案

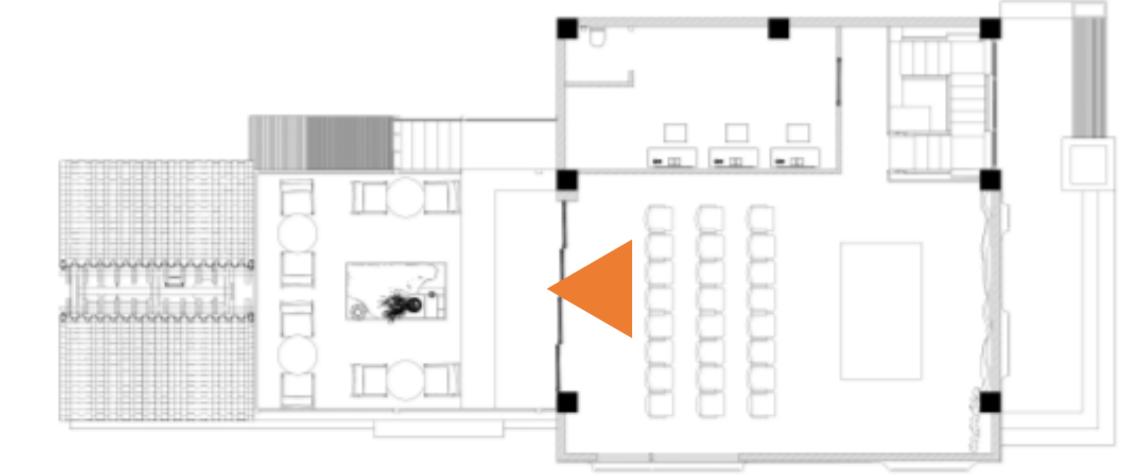

二楼剧场效果图



## 设计方案



二楼剧场效果图



## 设计方案



整体效果图

## 设计方案



整体效果图

# 设计方案



整体效果图

**THANKS**